

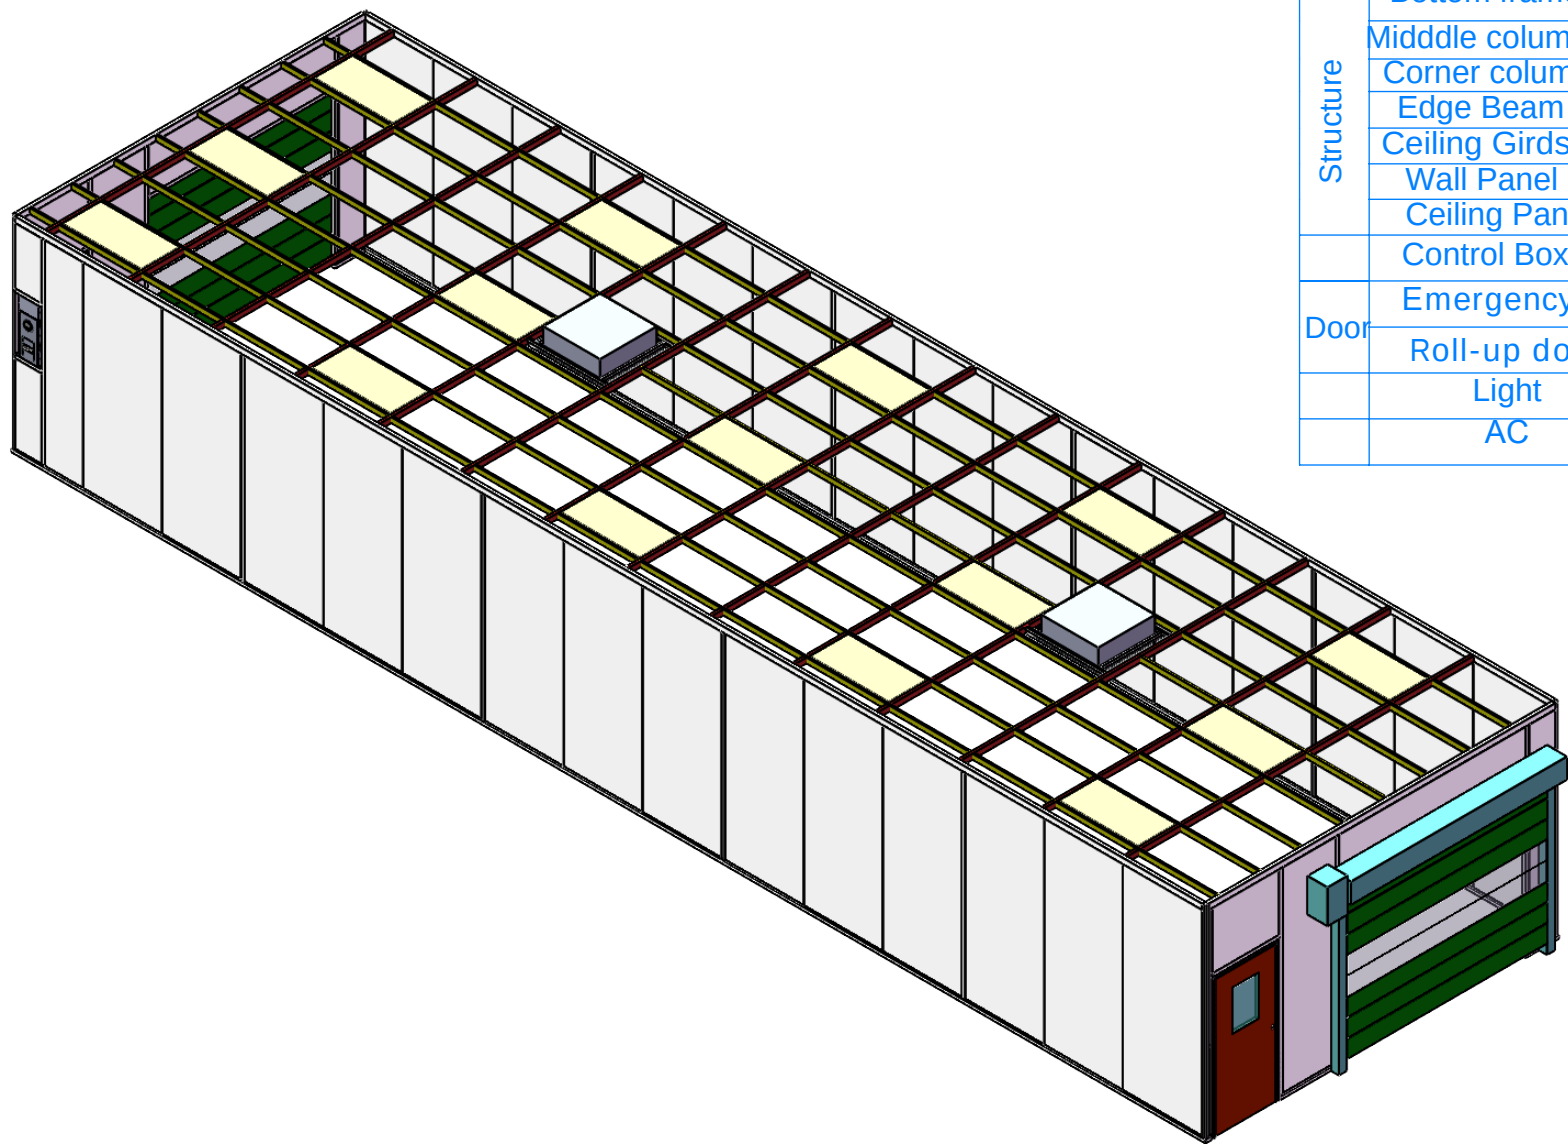
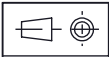
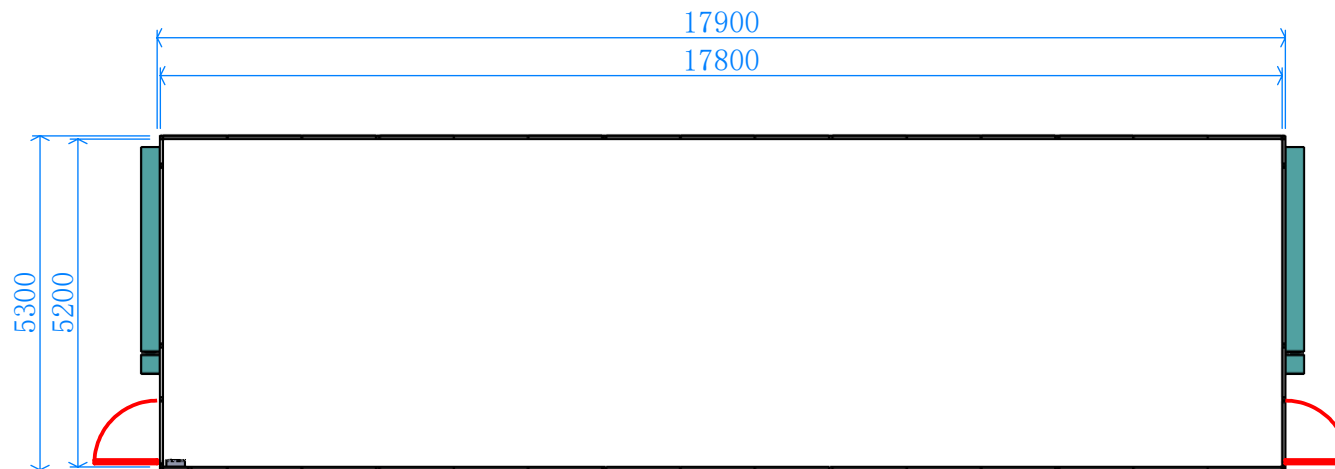
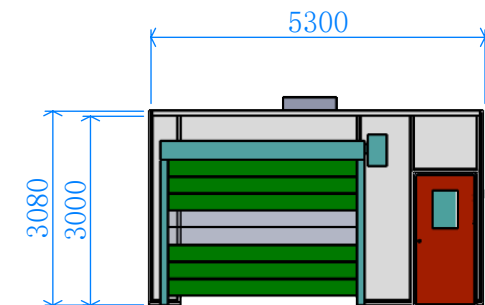



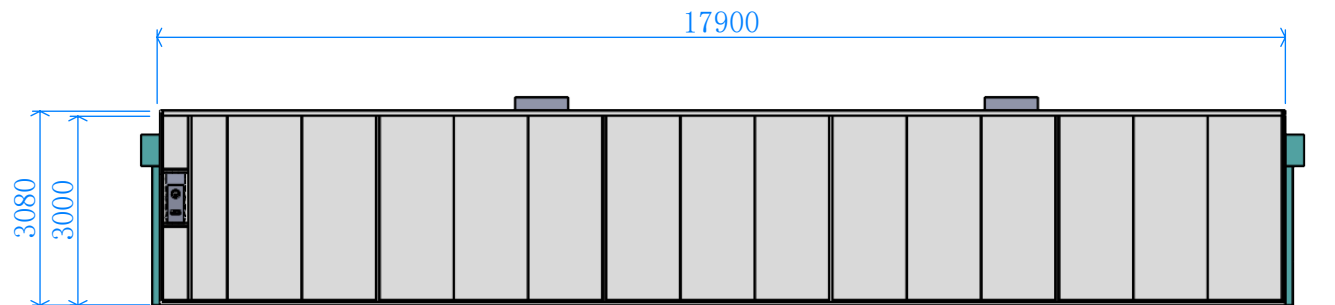


Type	Item	Size	QTY
Structure	Bottom frame	50x50 aluminum	
	Middle column	24/50x50 aluminum	
	Corner column	50x50 aluminum	
	Edge Beam	50x80 aluminum	
	Ceiling Girds	40x80/24x40 aluminum	
	Wall Panel	50mm	
	Ceiling Panel	50mm	
	Control Box	400x800	1
Door	Emergency Door	1000x2100	2
	Roll-up door	2800x2300	2
	Light	1200x600	13
	AC	950x950x306	2


		Date	AIRKEY ENVIROTECH CO., LTD	
		2026/1/8		
			Name:	
			ROOM FJ General View	
Production No.GHD251237			Scale	1:80

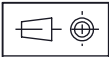


		Date	AIRKEY ENVIROTECH CO., LTD	
		2026/1/8		
			Name: ROOM FJ General View	
Production No.	GHD251237			Scale 1:120

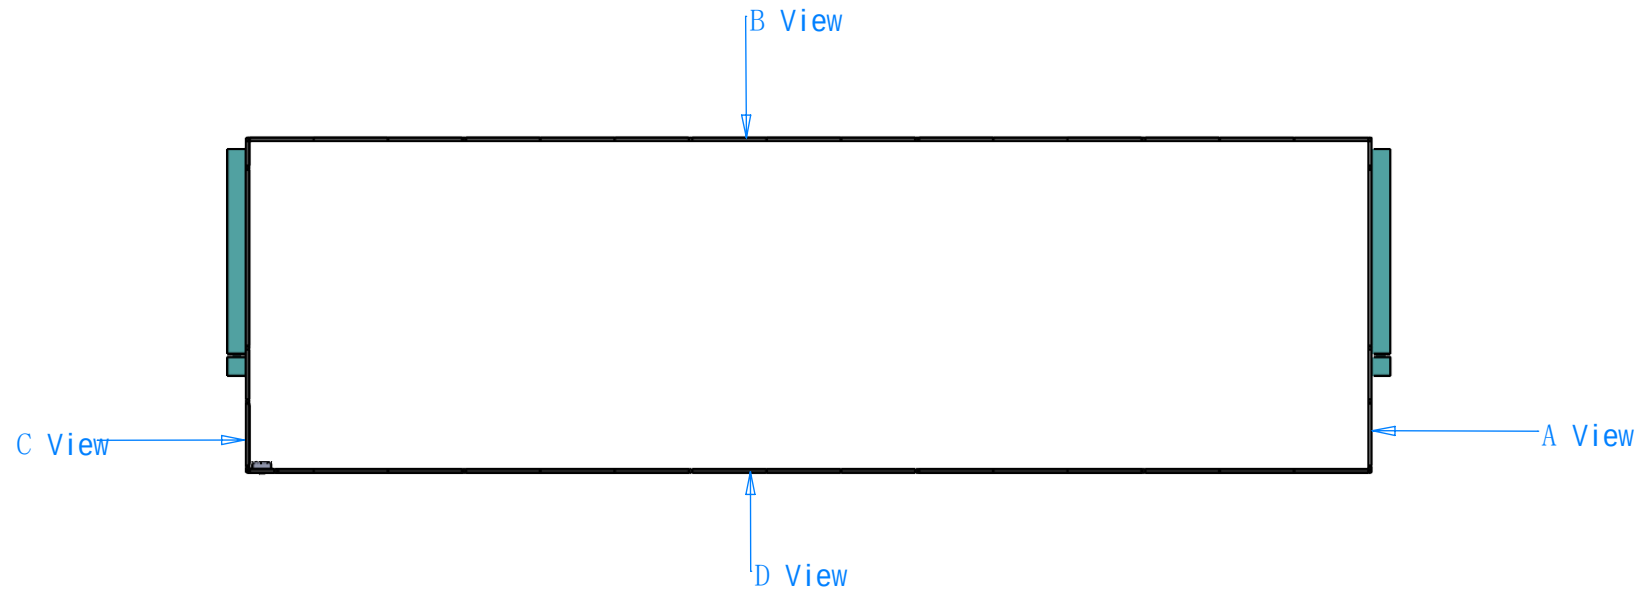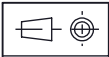


		Date	AIRKEY ENVIROTECH CO., LTD	
		2026/1/8		
			Name: ROOM FJ Sky View	
Production No.	GHD251237		Scale	1:120

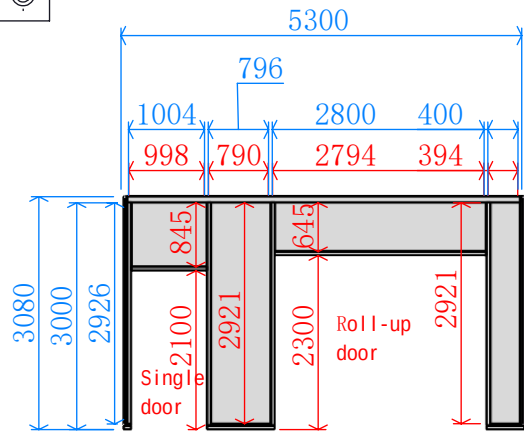


A View

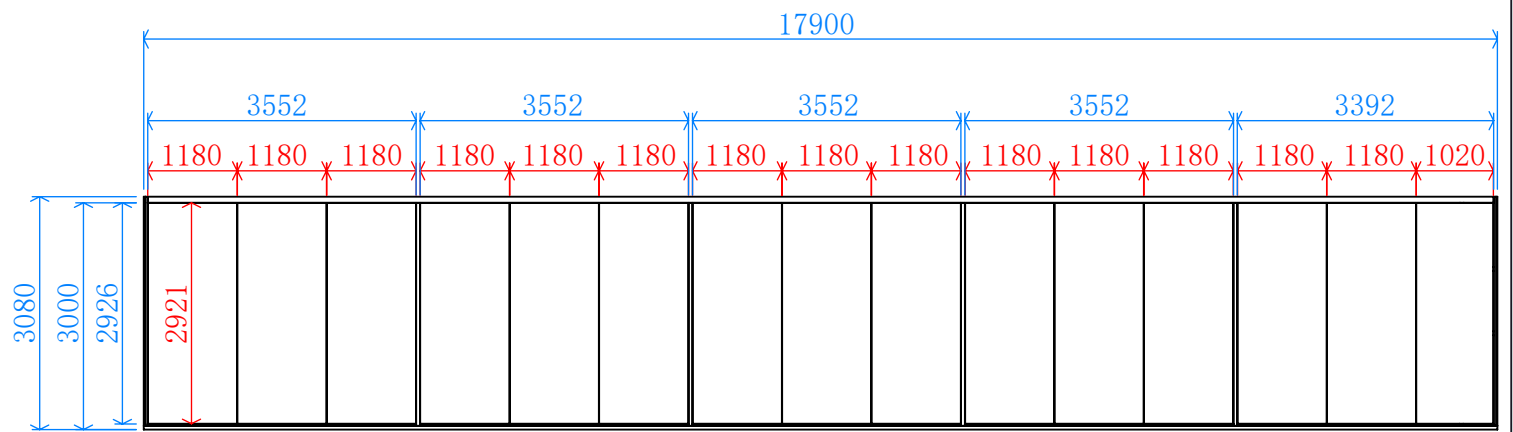

B View


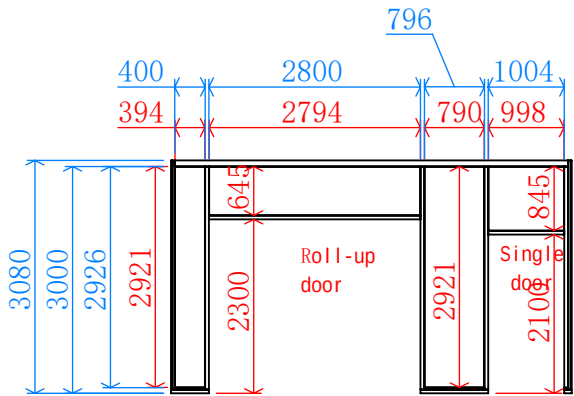


C View

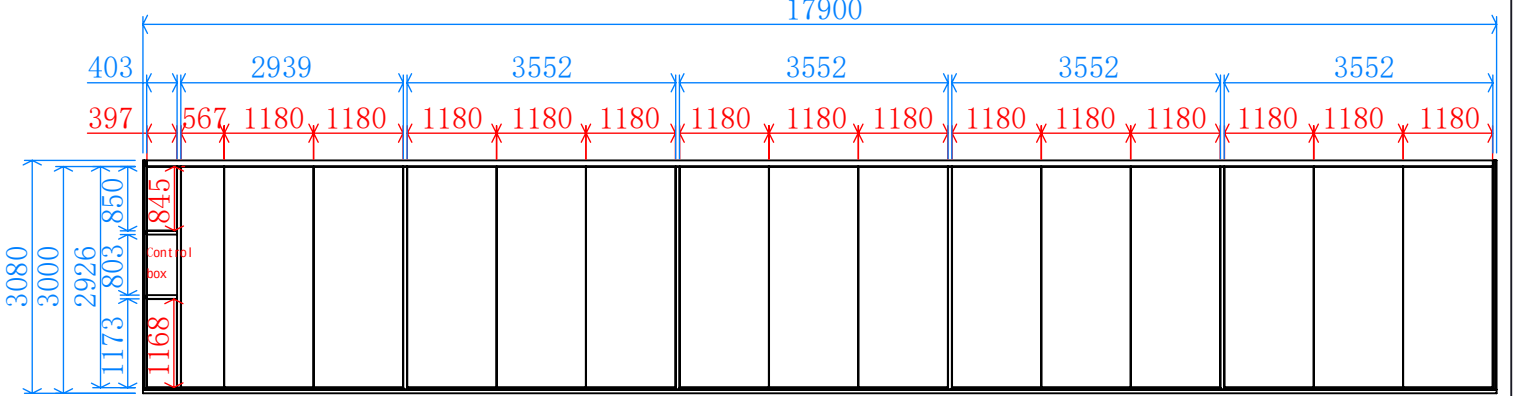

D View

		Date	AIRKEY ENVIROTECH CO., LTD
		2026/1/8	
			Name: ROOM FJ Elevations
Production No.GHD251237			Scale 1:100

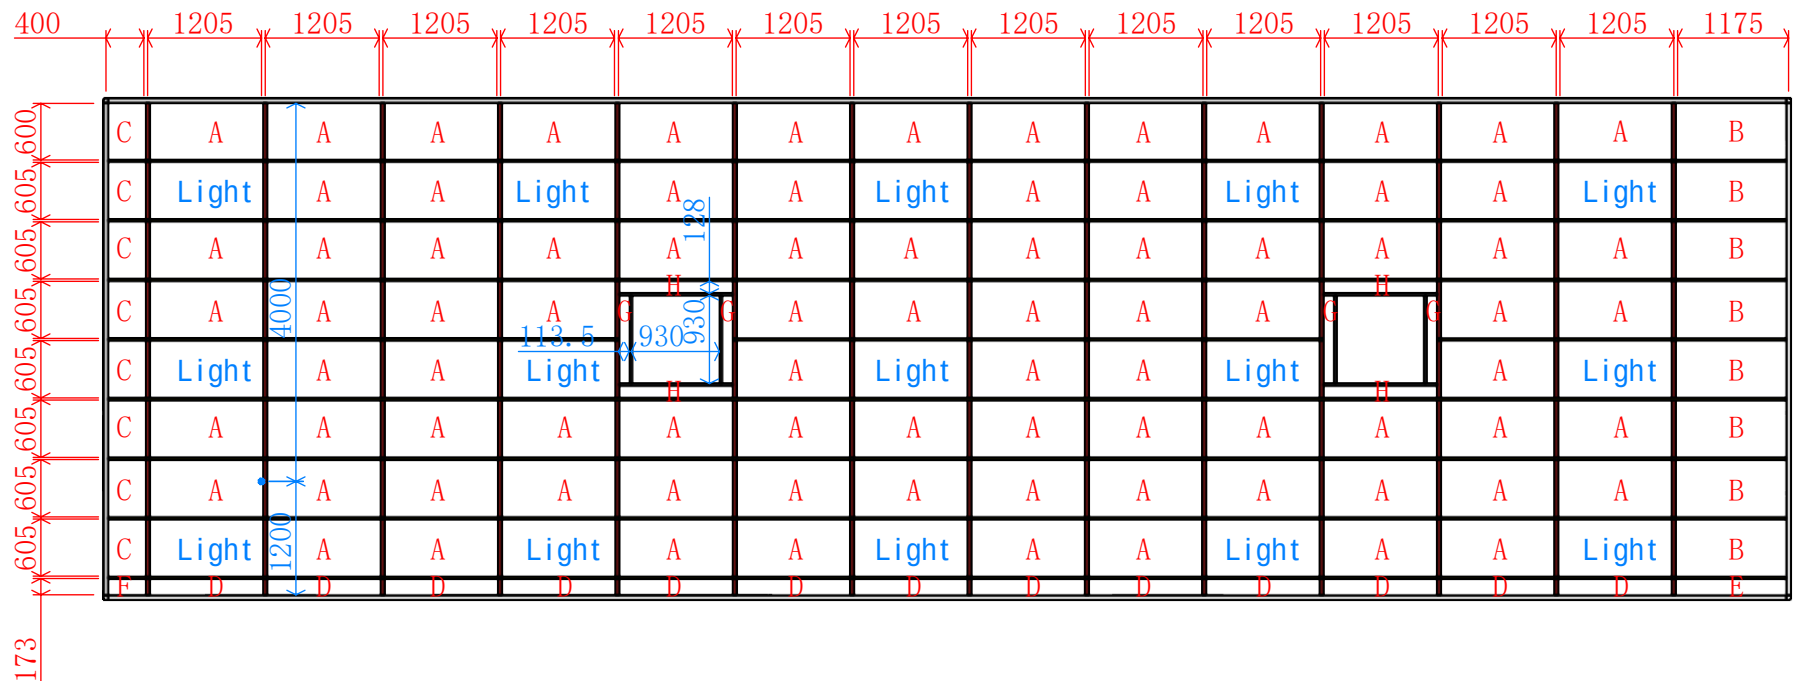
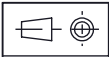


Ceiling Panels		
Label	Size/mm	Qty
A	1190x590	85
B	1160x590	8
C	385x590	8
D	1190x160	13
E	1160x160	1
F	385x160	1
G	100x915	4
H	1190x115	4

40X80 Main Ceiling Gird		
Label	Size/mm	Qty
MG4080-1	4000	14
MG4080-2	1200	14

24x40x65T Sub-ceiling Gird		
Label	Size/mm	QTY
MG2440-1	1205	106
MG2440-2	1175	8
MG2440-3	930	4
MG2440-4	400	8



		Date	AIRKEY ENVIROTECH CO., LTD		
		2026/1/8			
			Name:		
			ROOM FJ Ceiling Panels & Grids		
Production No.GHD251237				Scale	1:80

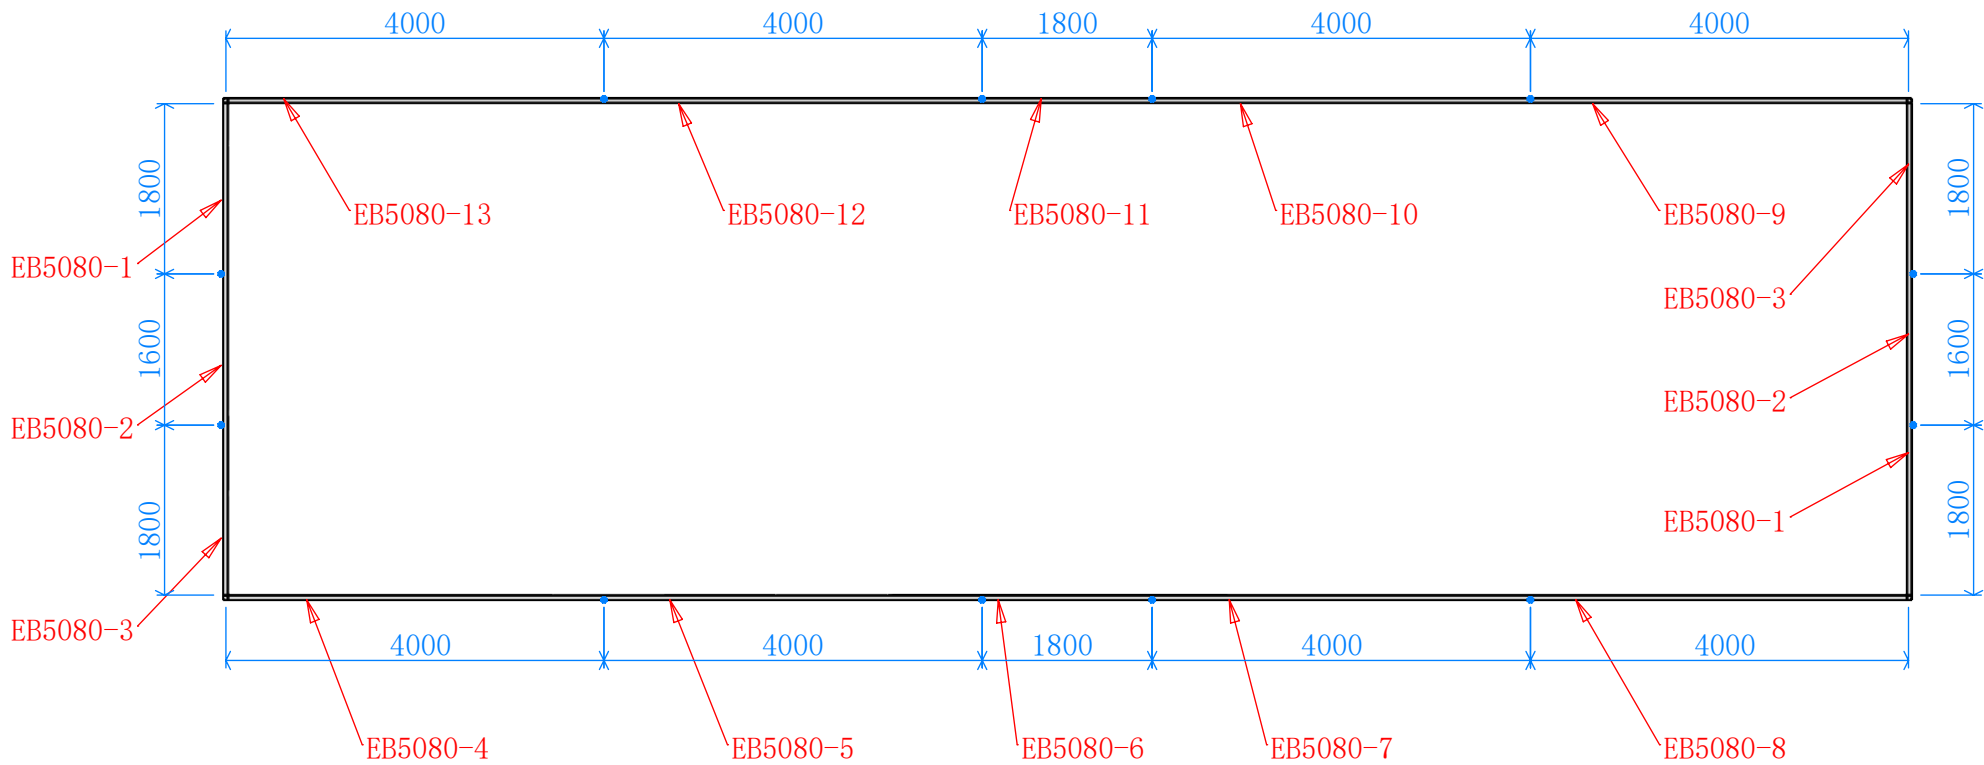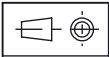



50*80 Edge Beam

Label	Length/mm	Qty
EB5080-1	1800	2
EB5080-2	1600	2
EB5080-3	1800	2
EB5080-4	4000	1
EB5080-5	4000	1
EB5080-6	1800	1
EB5080-7	4000	1
EB5080-8	4000	1
EB5080-9	4000	1
EB5080-10	4000	1
EB5080-11	1800	1
EB5080-12	4000	1
EB5080-13	4000	1


		Date	AIRKEY ENVIROTECH CO., LTD	
		2026/1/8		
			Name : ROOM FJ Edge Beams	
Production No.	GHD251237		Scale	1:80

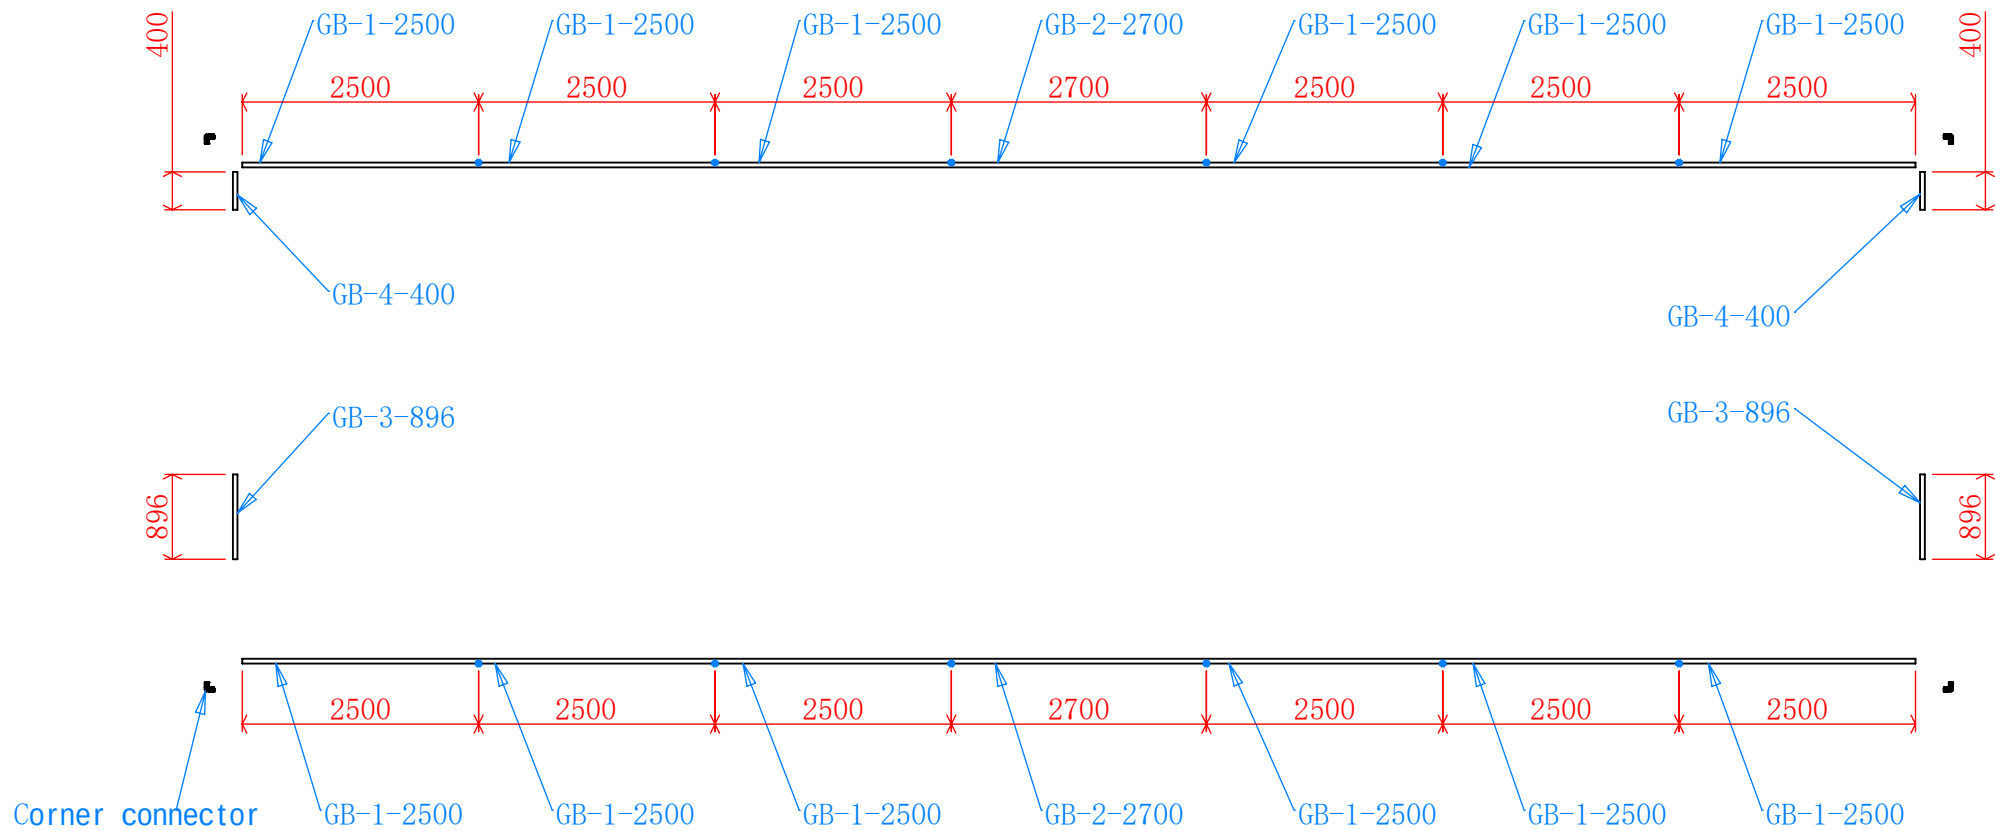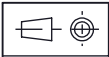



		Date	AIRKEY ENVIROTECH CO., LTD	
		2026/1/8		
			Name: ROOM FJ Bottom Frames	
Production No.	GHD251237		Scale	1:80

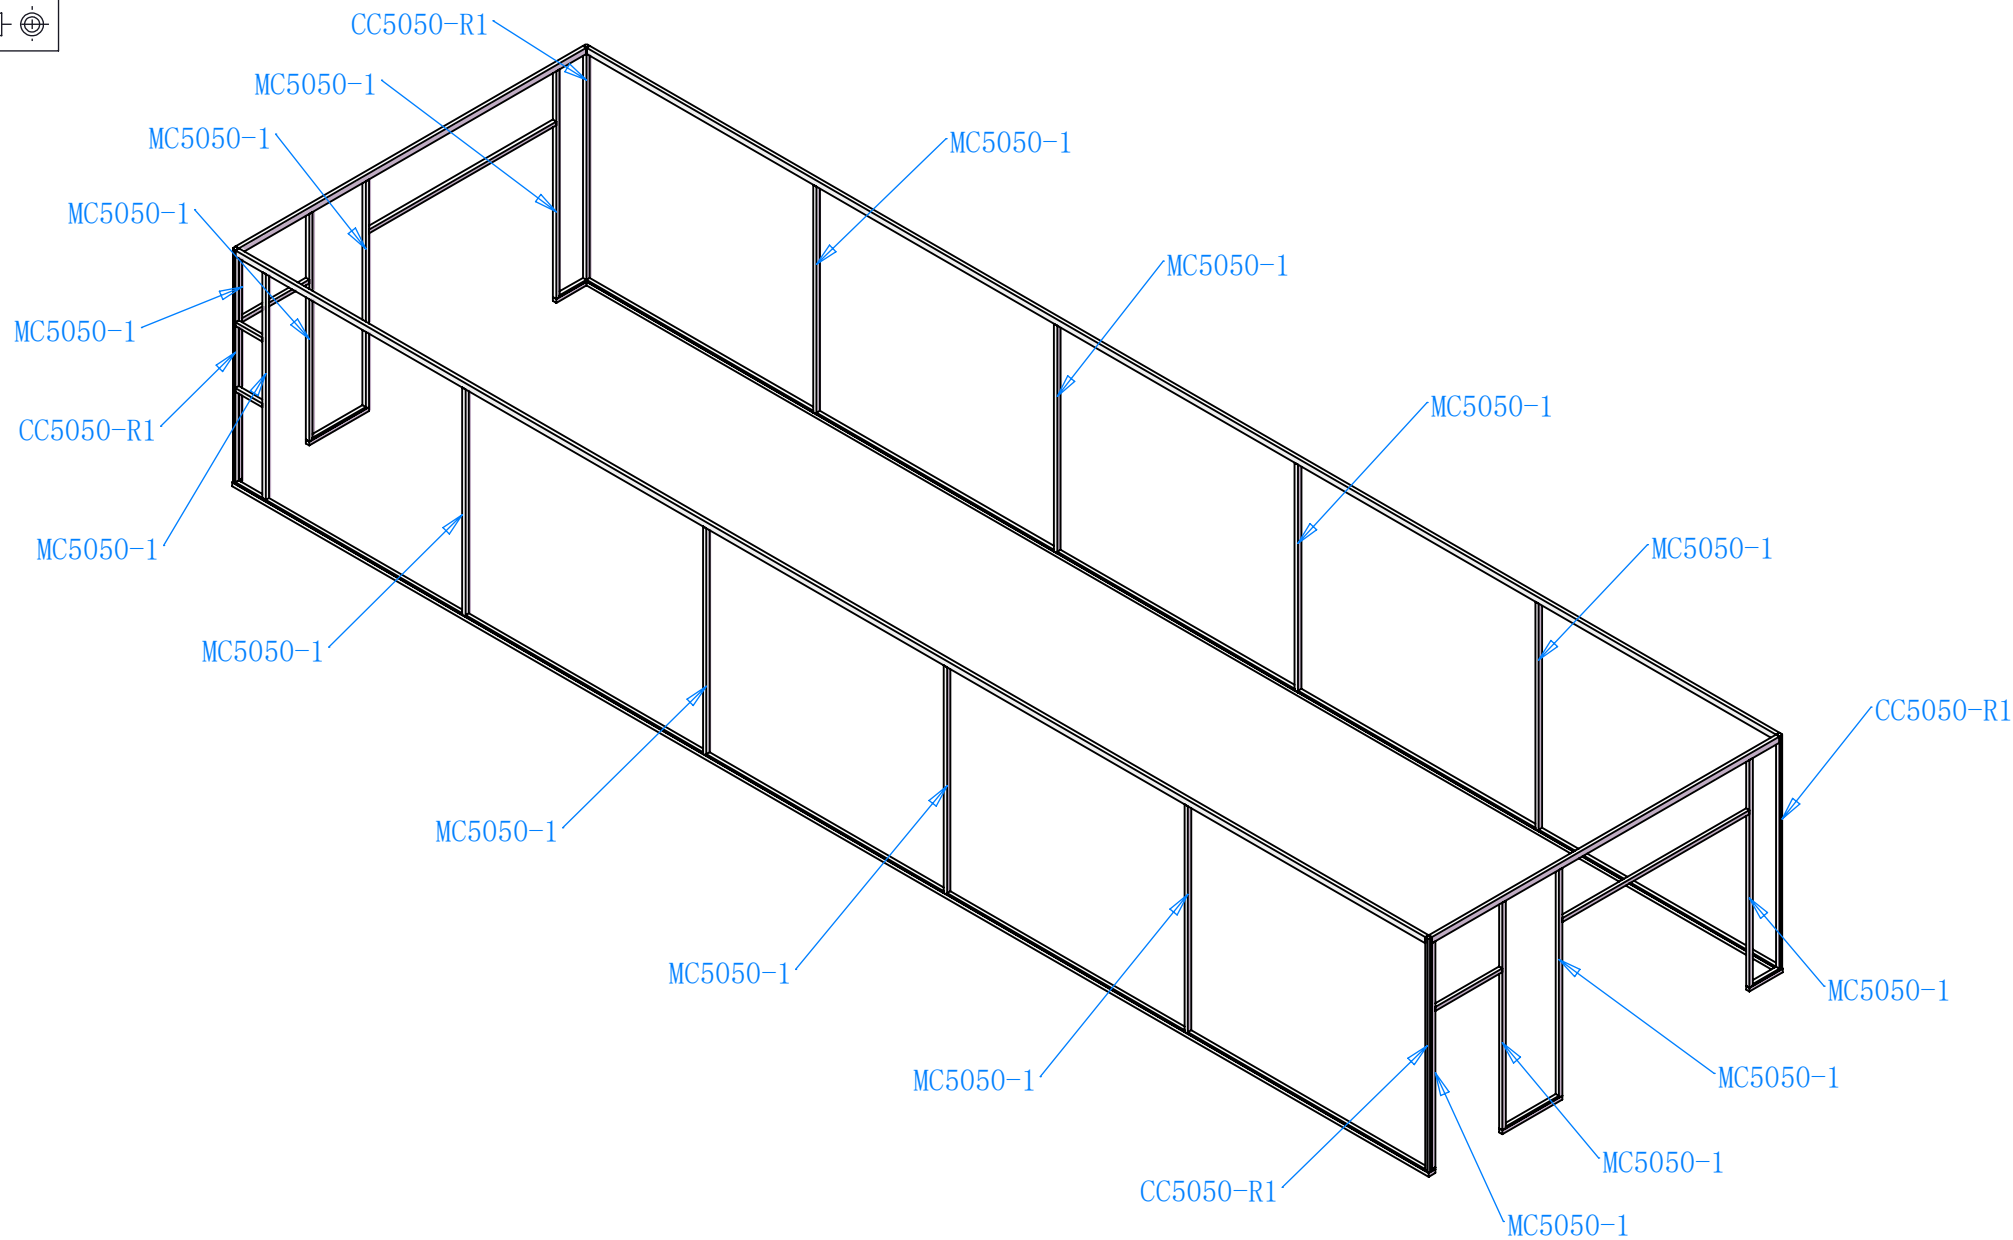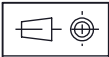




		Date	AIRKEY ENVIROTECH CO., LTD	
		2026/1/8		
			Name: ROOM FJ Column Frames	
Production No.	GHD251237		Scale	1:80

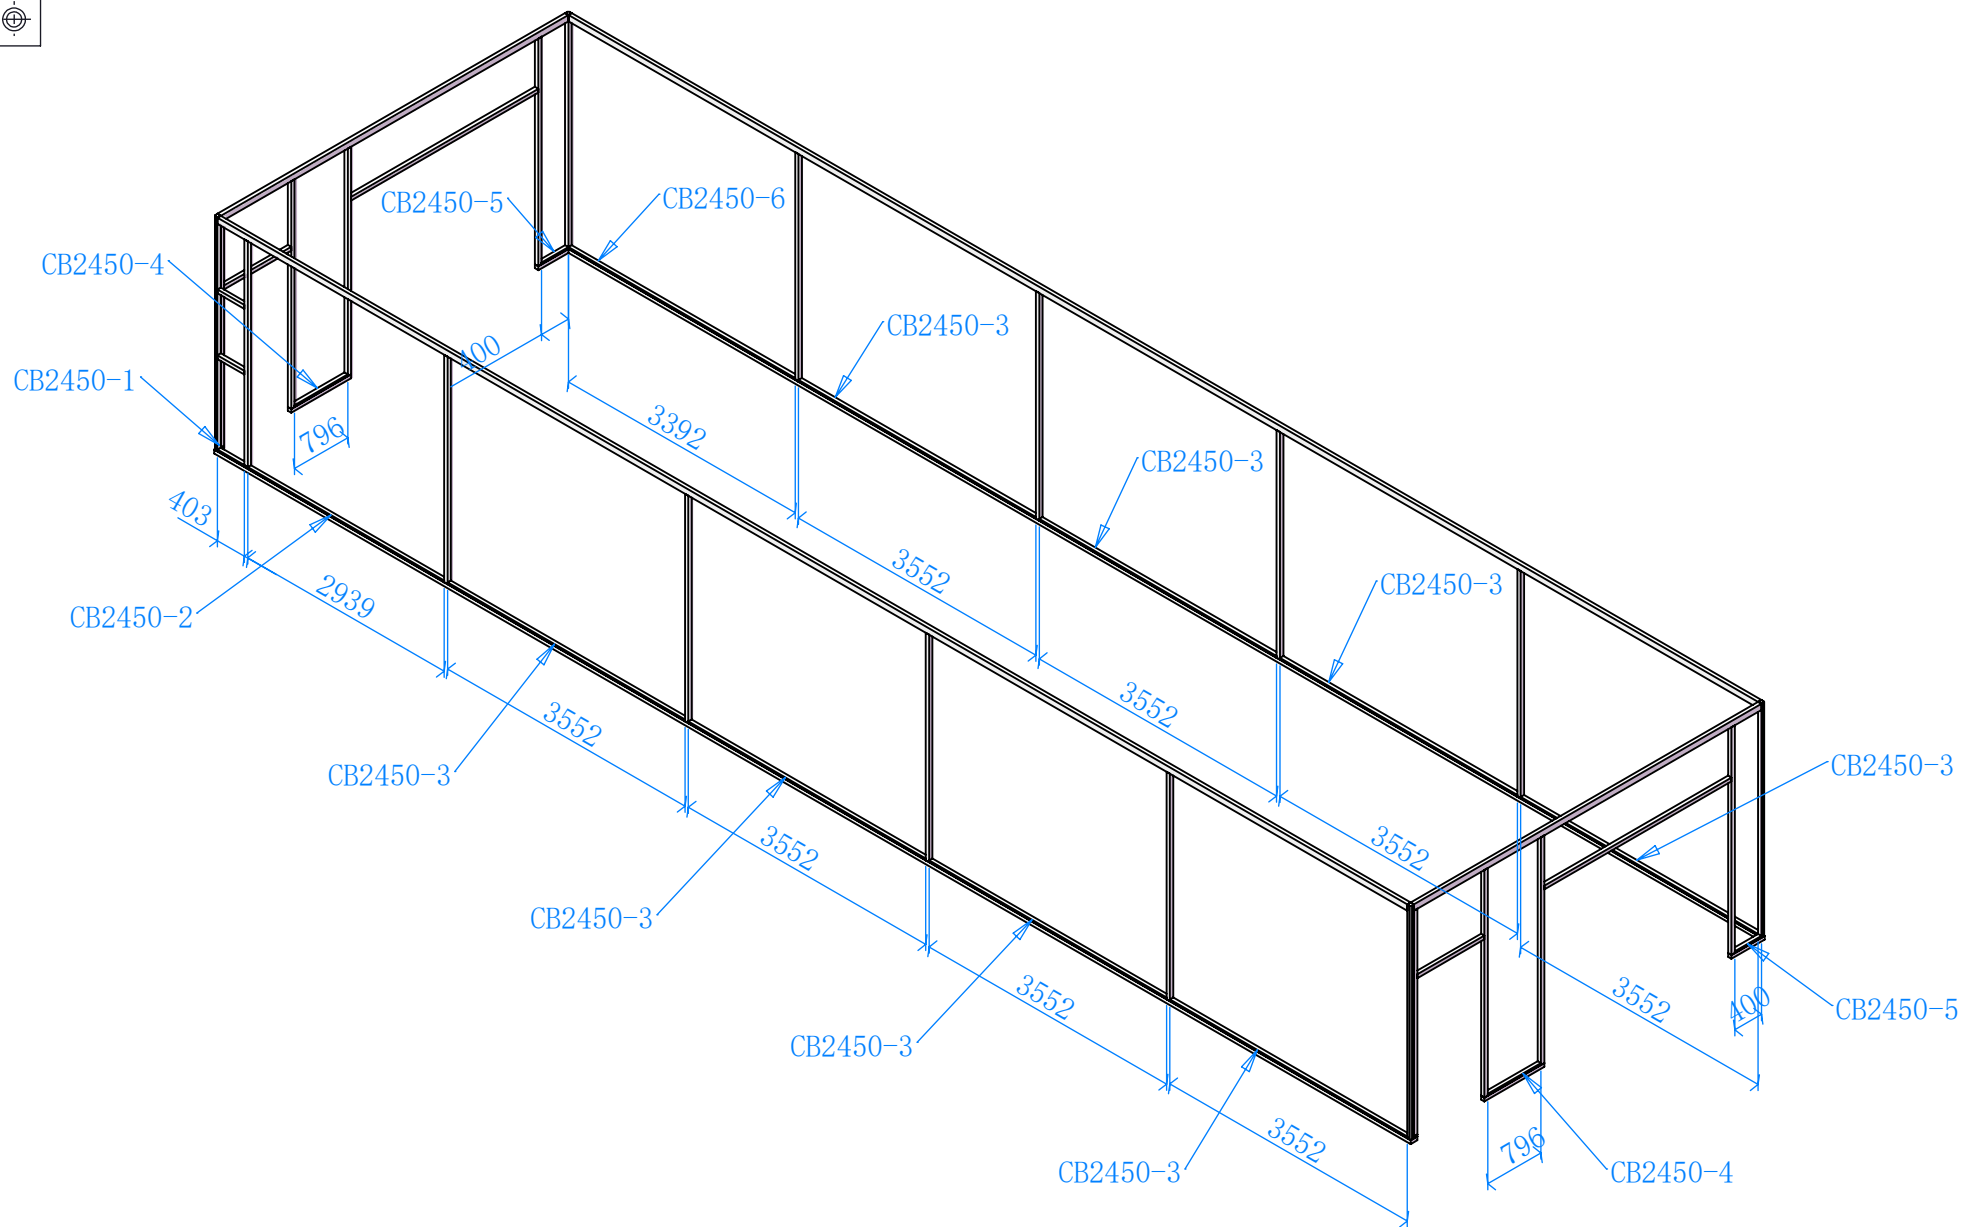

		Date	AIRKEY ENVIROTECH CO., LTD		
		2026/1/8			
			Name: ROOM FJ Bracing Frames		
Production No.	GHD251237		Scale	1:80	

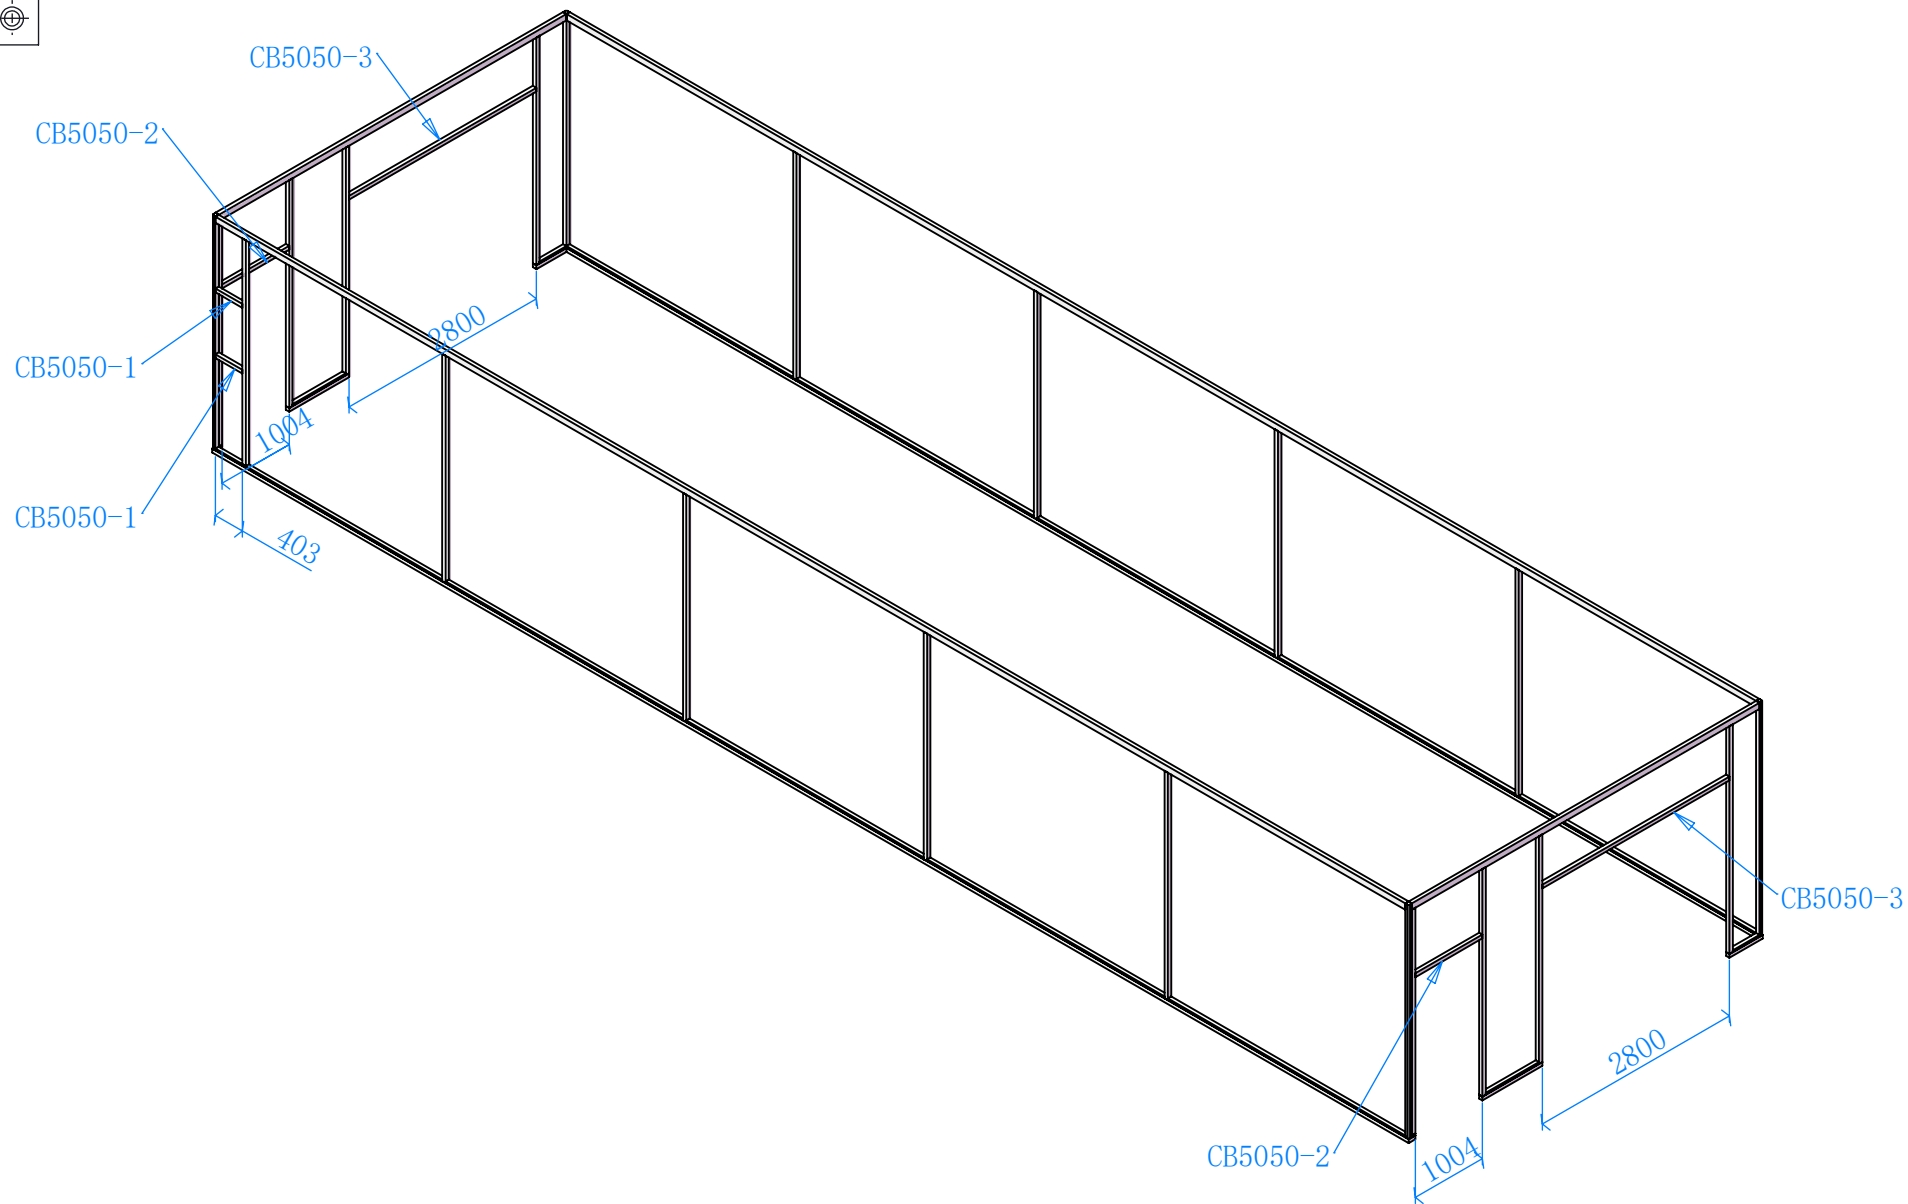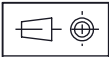

		Date	AIRKEY ENVIROTECH CO., LTD		
		2026/1/8			
			Name: ROOM FJ Bracing Frames		
Production No.	GHD251237			Scale	1:80

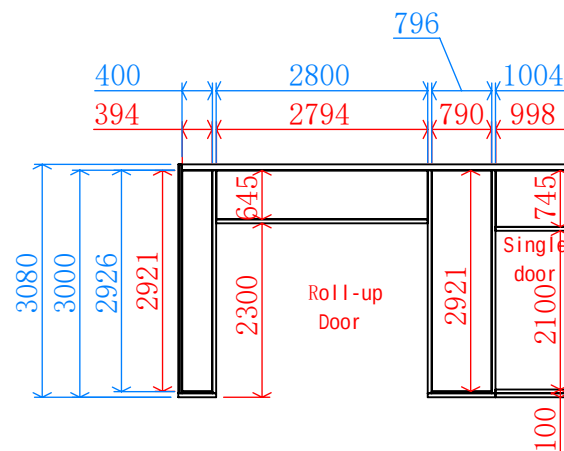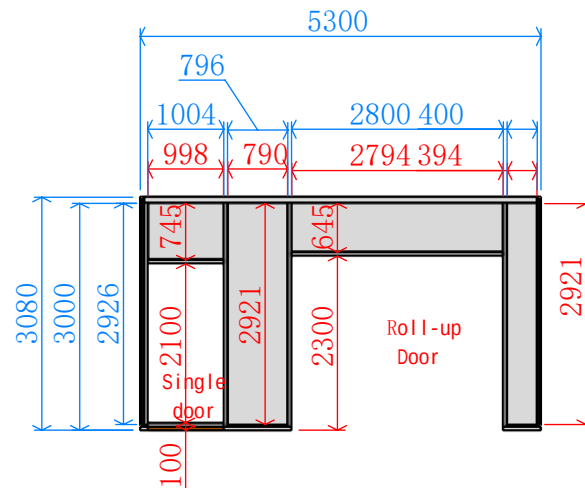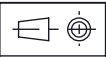


		Date	AIRKEY ENVIROTECH CO., LTD	
		2026/1/8		
			Name: ROOM FJ Elevation	
Production	No.GHD251237			Scale 1:100



Note:


1. Install trusses first and then ceiling panels, lights, AC
2. Insert M8 screw into the main ceiling grid;
3. Fix with M8 nut

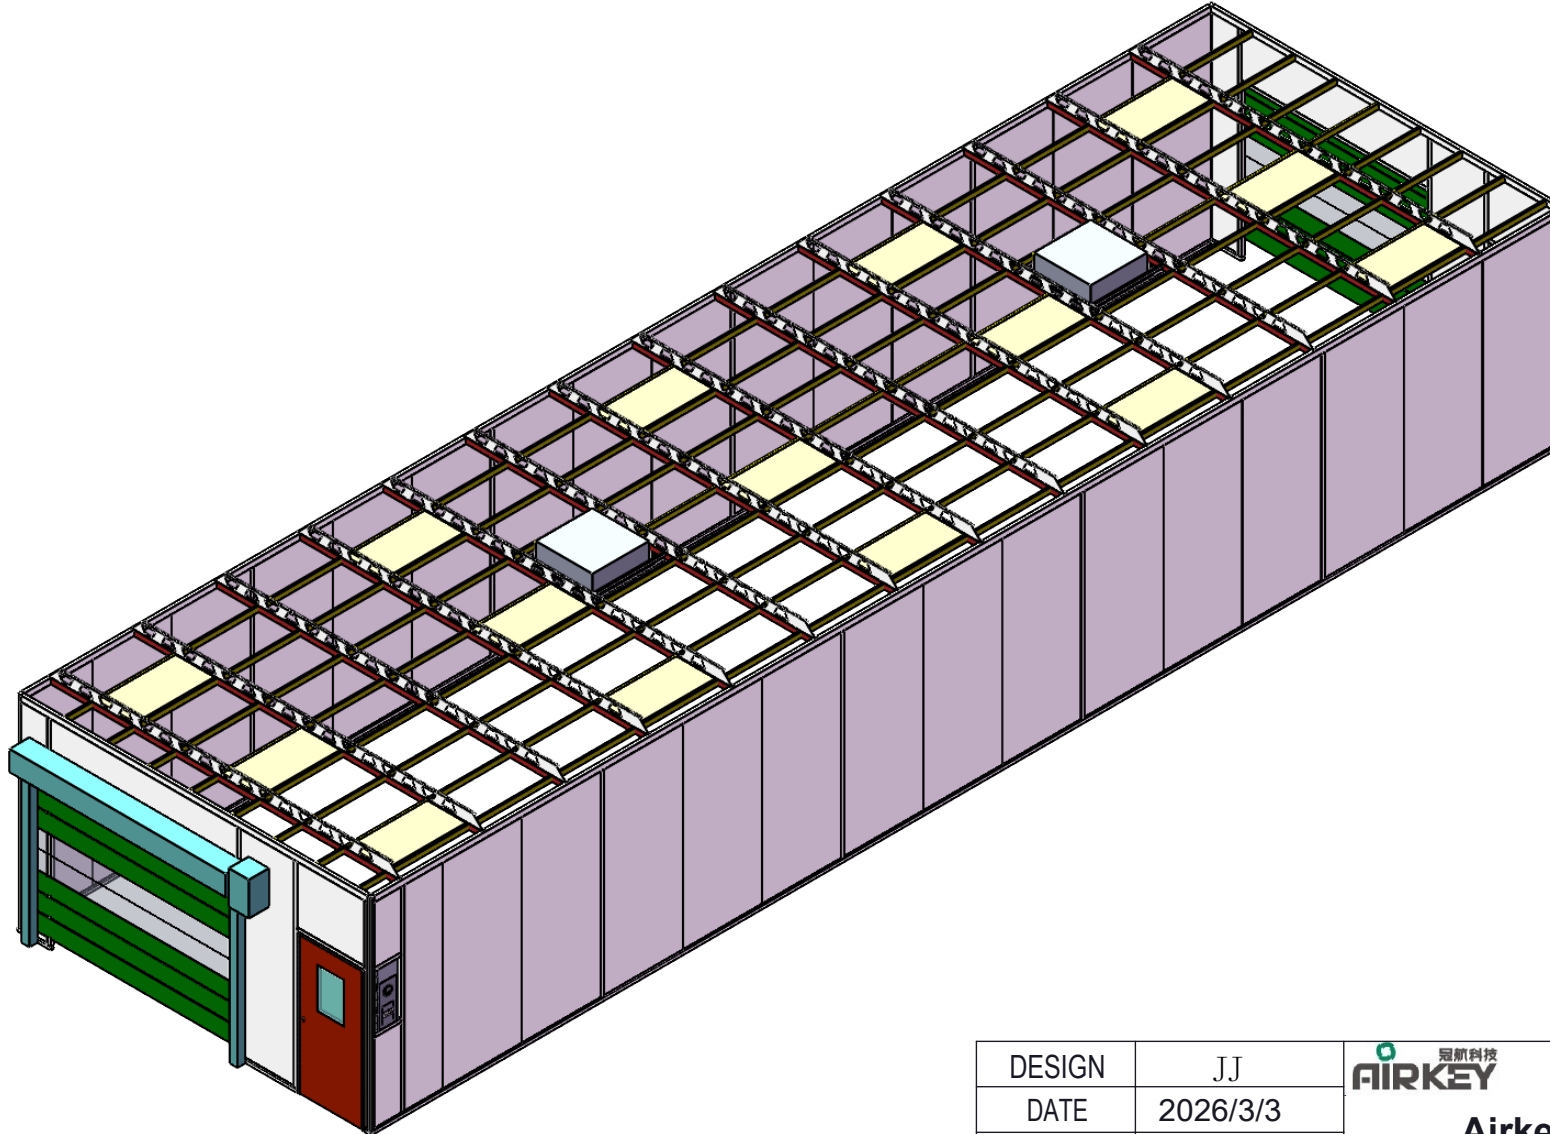



DESIGN	JJ	 Airkey Envirotech Co.,Ltd Item : Location of Truss
DATE	2026/3/3	
REVIEW		
RATIO	1:500	
DWG No.	2	





Truss Installation Illustration

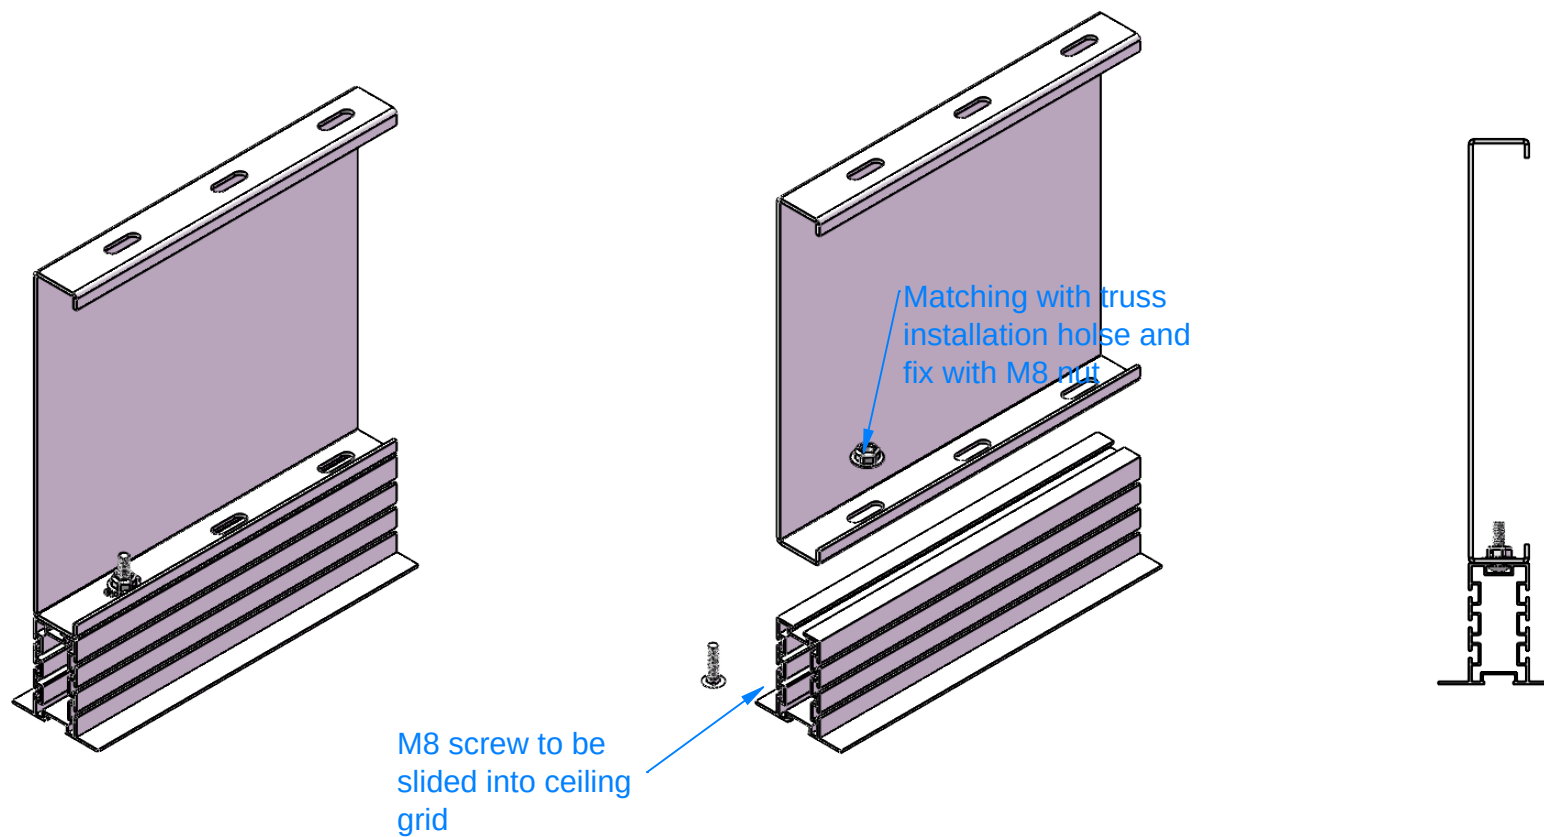


DESIGN	JJ	 Airkey Envirotech Co.,Ltd Item : Truss Installation
DATE	2026/3/3	
REVIEW		
RATIO	1:500	
DWG No.	2	

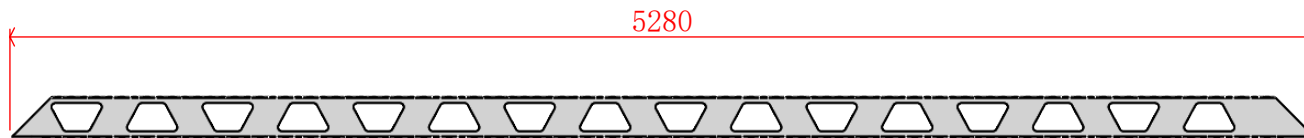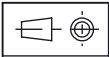

160 C-shaped truss
Each truss with 5 screws and nuts
5280mm * 14pcs(18kg/1pcs)

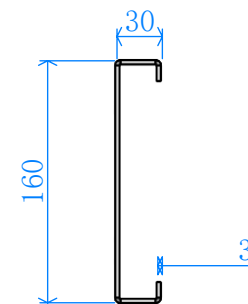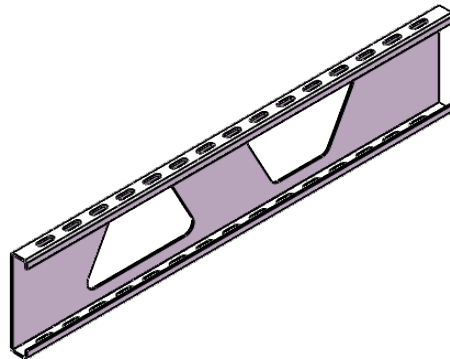


DESIGN	CJJ	 Airkey Envirotech Co.,Ltd Item : Truss Specification
DATE	2026/3/3	
REVIEW		
RATIO	1:10	
DWG No.	3	

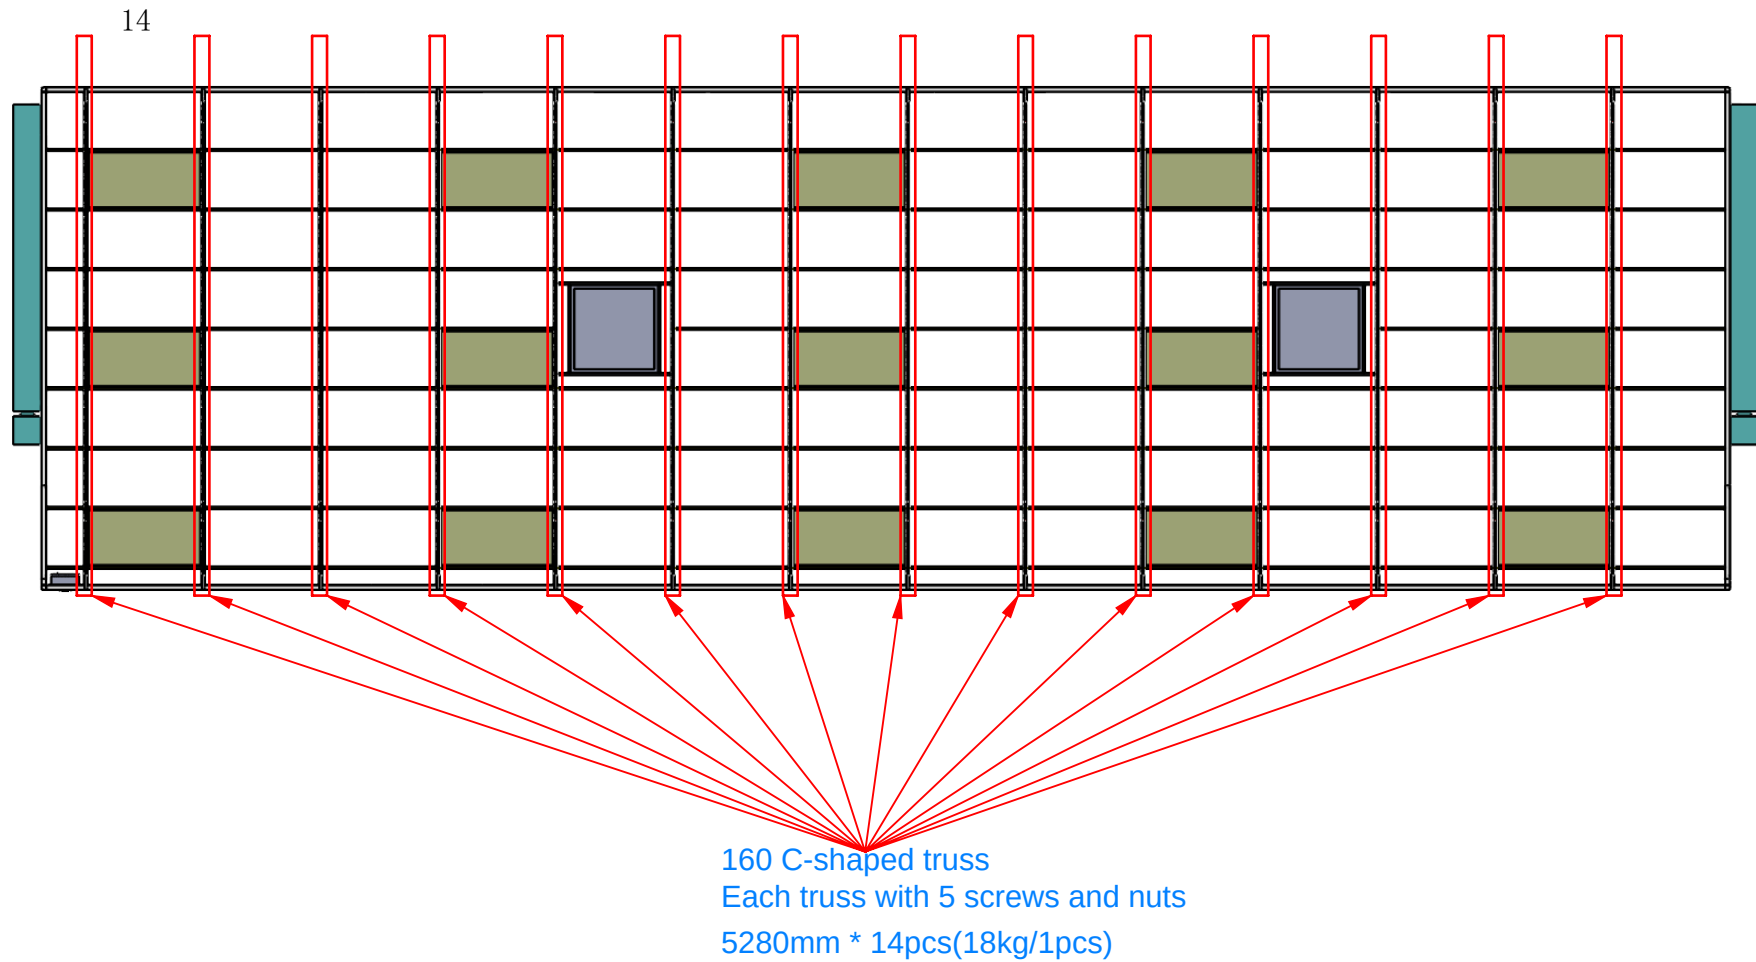

DESIGN	JJ	 Airkey Envirotech Co.,Ltd Item : truss installation
DATE	2026/3/3	
REVIEW		
RATIO	1:500	
DWG No.	4	



Edges of truss onto edge beams

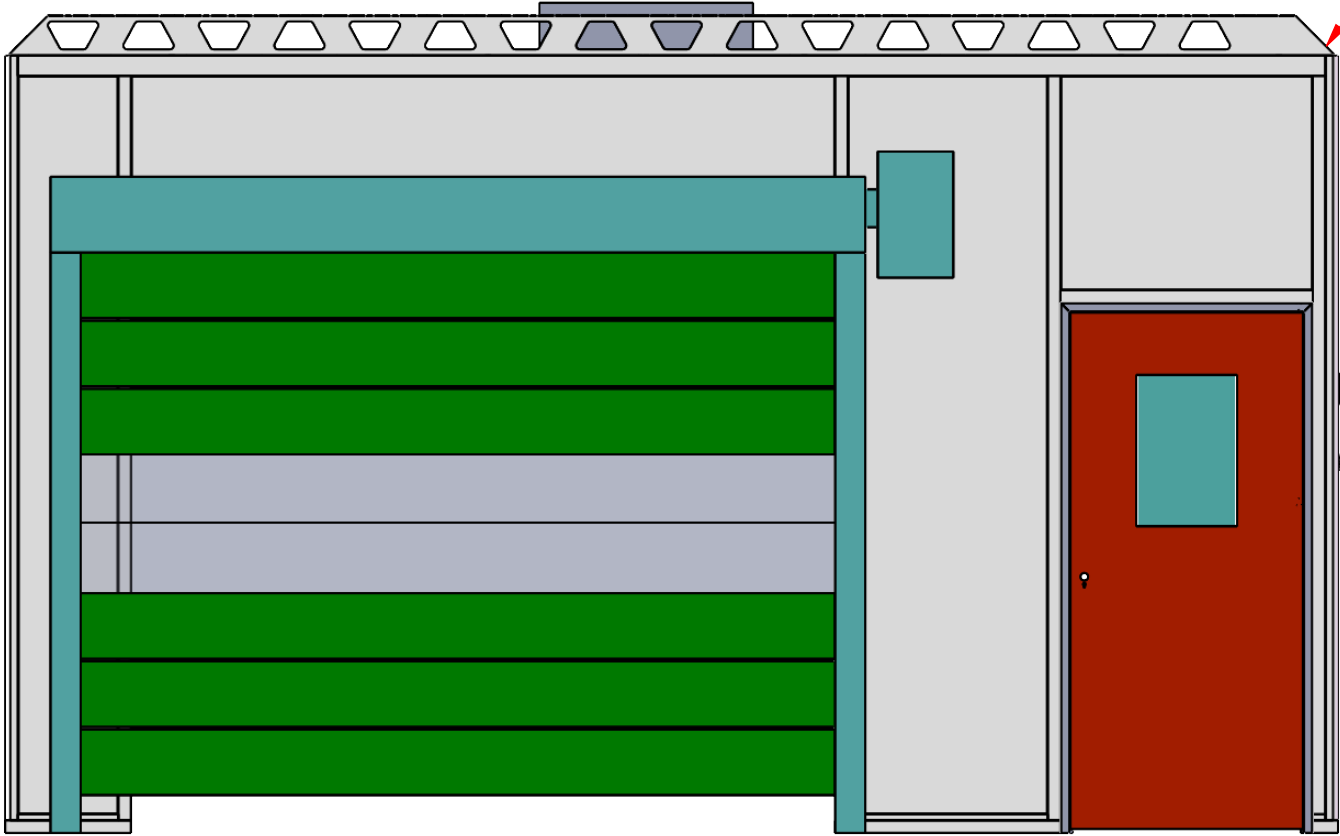

DESIGN	JJ	 Airkey Envirotech Co.,Ltd Item : truss installation
DATE	2026/3/3	
REVIEW		
RATIO	1:500	
DWG No.	5	