


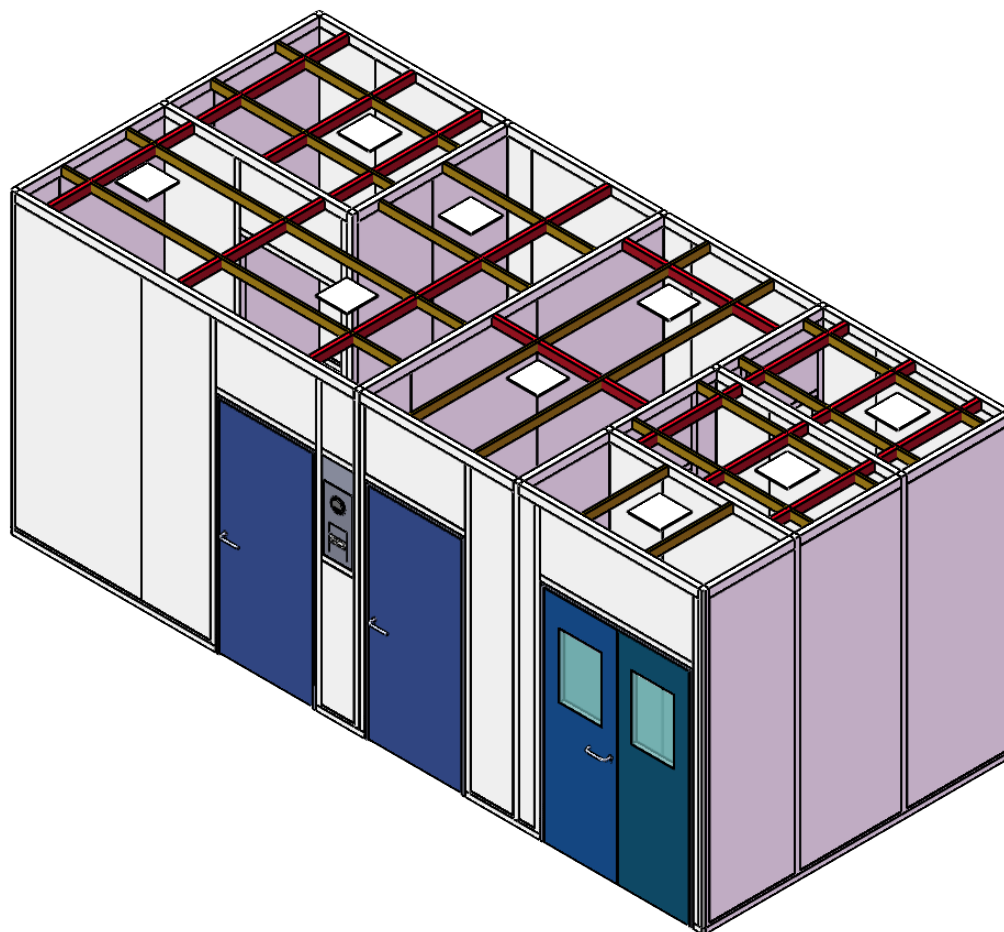
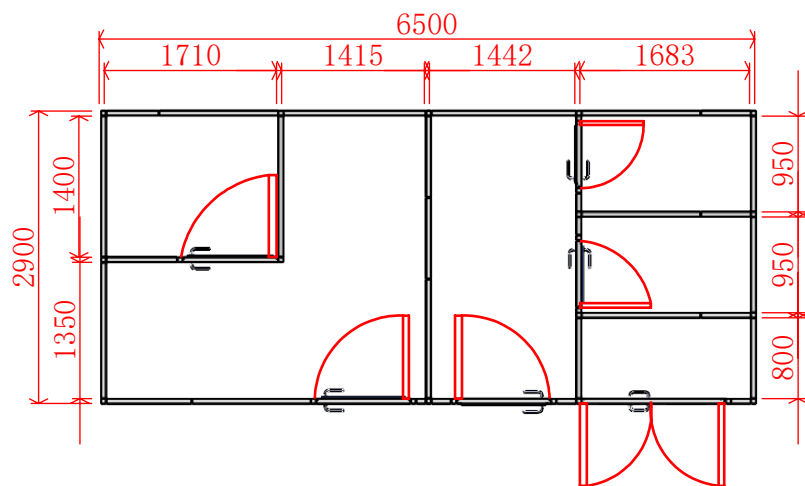
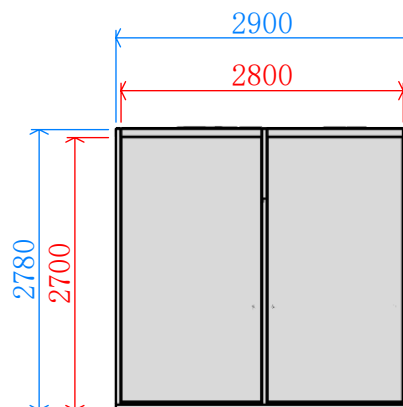


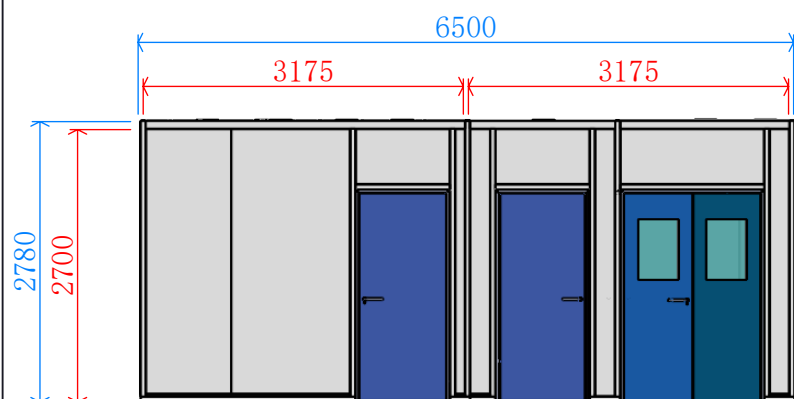

DESIGN	FYJ	 Airkey Envirotech Co.,Ltd
DATE	2026/1/8	
REVIEW		
RATIO	1:50	Item : FSP-N-A19 (9. 2+9. 2) -F
DWG No.	1	


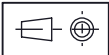


Cleanroom Parameter	
Model	FSP-N-A19(9. 2+9. 2)-F
Clean class	
Normal operation	3Ph, 4W+E, 400V, 50Hz
Emergency	AC, Single Phase 220V/50HZ
Max Power Consumption	400W(not including airshower power)
Construction	Aluminum frame, Rock wool sandwich panel wall


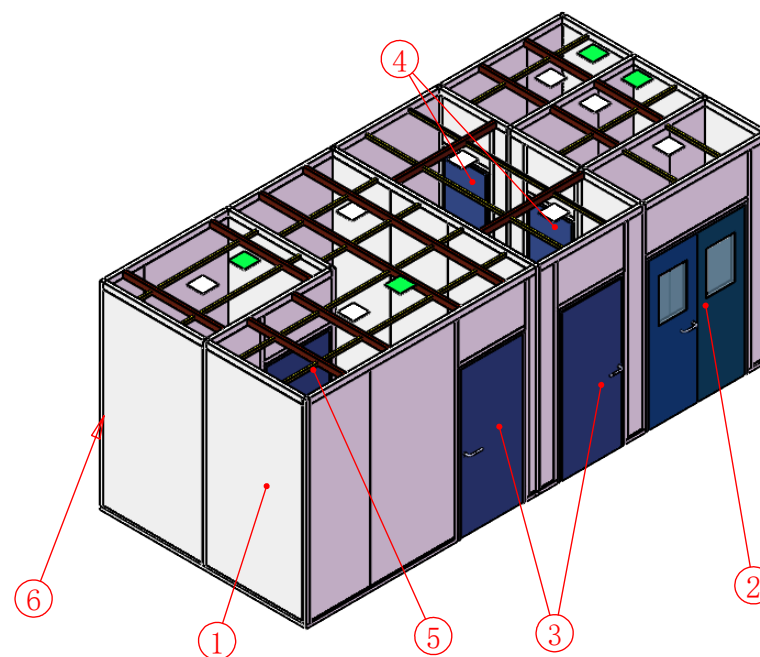


8	LED Panel light	9 set		
7	Exhaust fan	4 Set		
6	Aluminum frame	1 Set		
5	Single door-3	1 PCS	W952*H2100	
4	Single door-2	2 PCS	W666*H2100	
3	Single door-1	2 PCS	W940*H2100	
2	Double door-1	1 PCS	W1433*H2100	
1	50mm thick manual sandwich panel	1 Set		
No.	Item	QTY	Parameter	NOTE


DESIGN	FYJ	 Airkey Envirotech Co.,Ltd
DATE	2026/1/8	
REVIEW		
RATIO	1:100	Item : FSP-N-A19(9. 2+9. 2)-F
DWG No.	2	

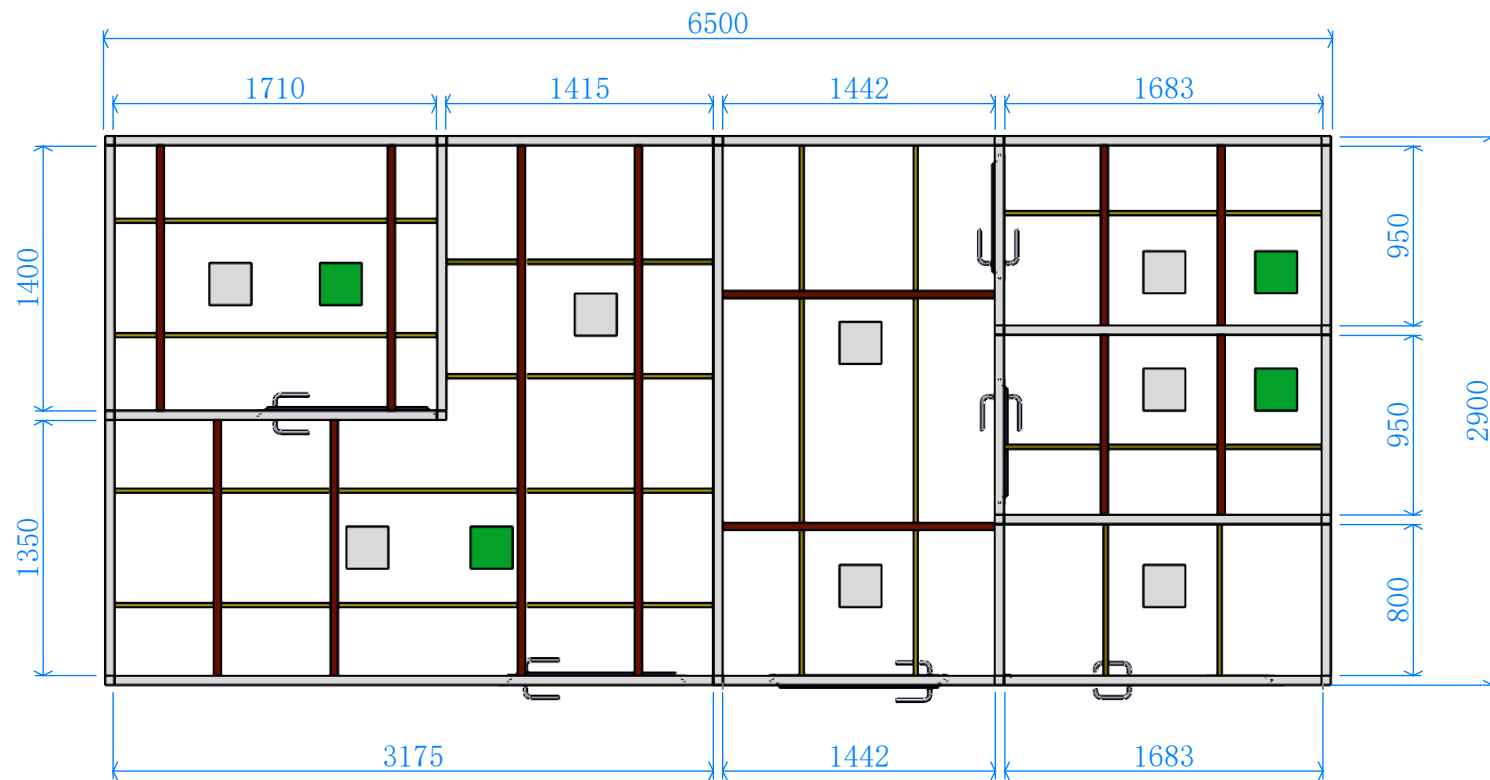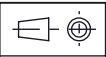


DESIGN	FYJ	 Airkey Envirotech Co.,Ltd
DATE	2026/1/8	
REVIEW		
RATIO	1:100	Item : FSP-N-A19 (9. 2+9. 2) -F
DWG No.	3	

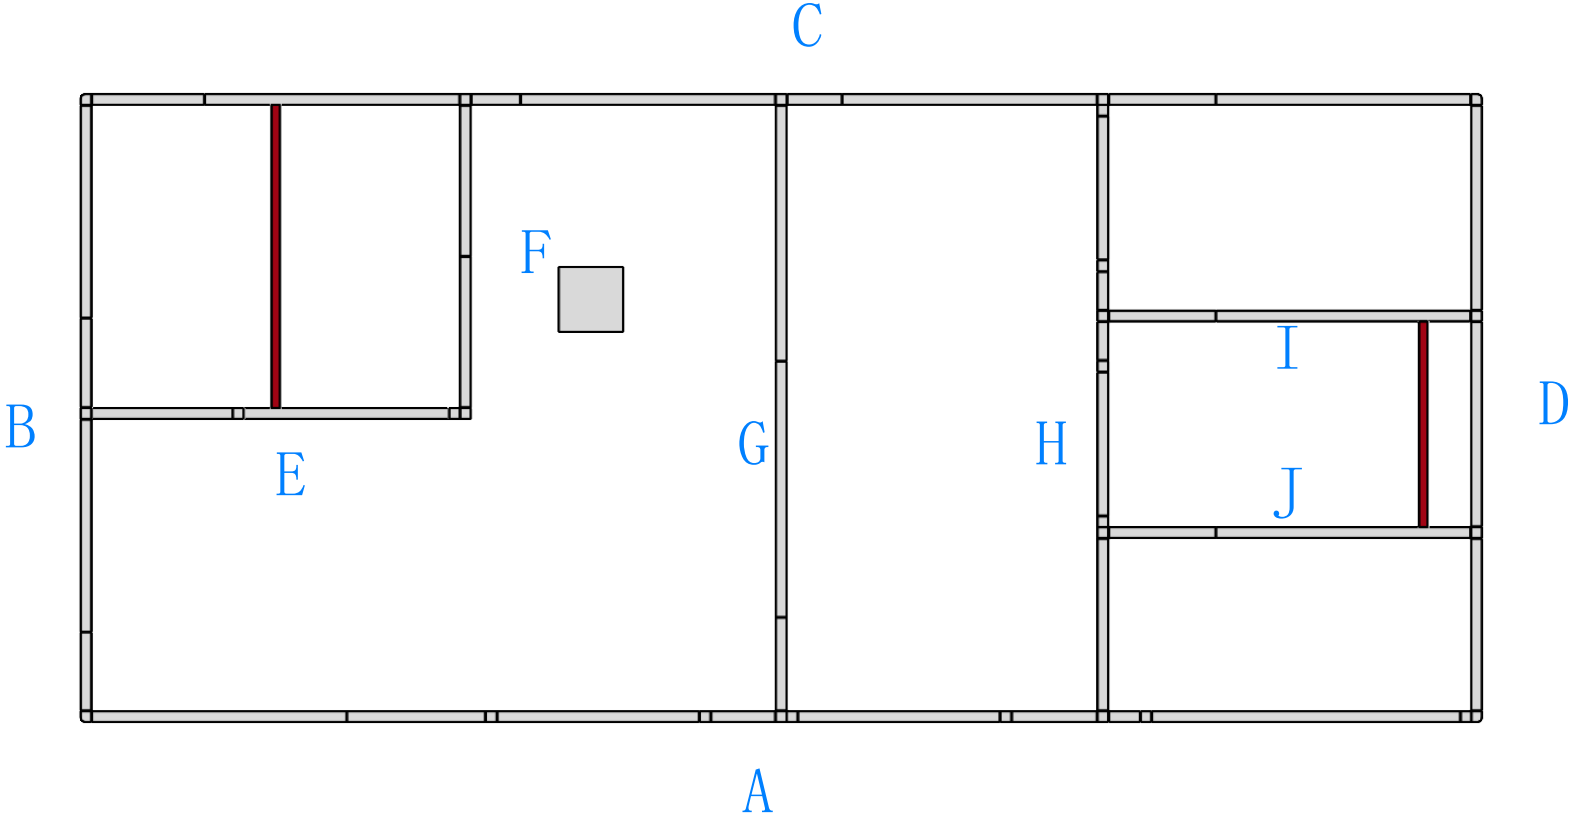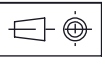

DESIGN	FYJ	 Airkey Envirotech Co.,Ltd
DATE	2026/1/8	
REVIEW		
RATIO	1:35	Item : FSP-N-A19 (9. 2+9. 2) -F
DWG No.	4	


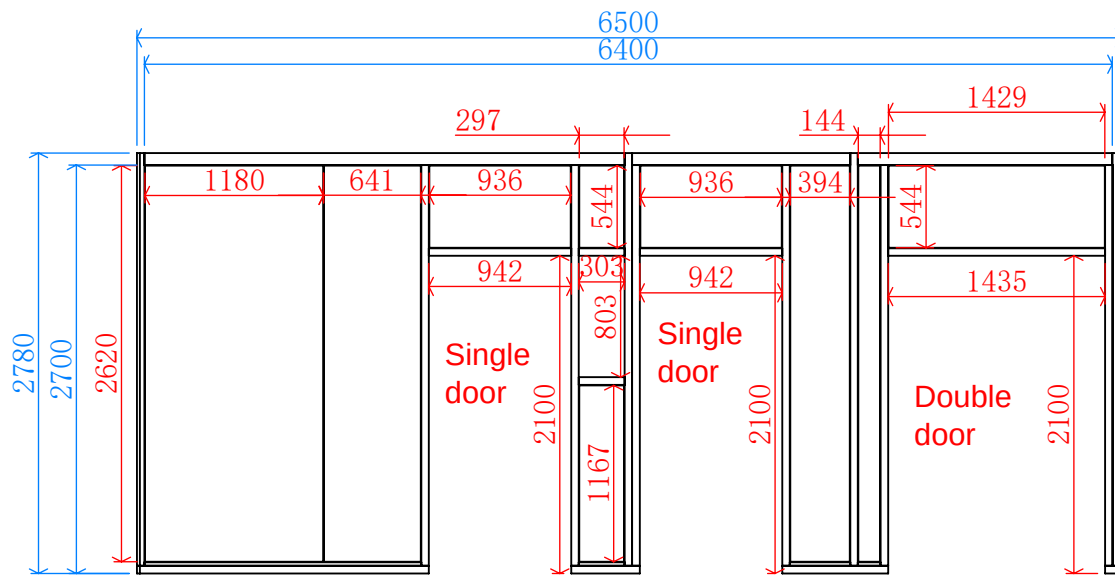


A

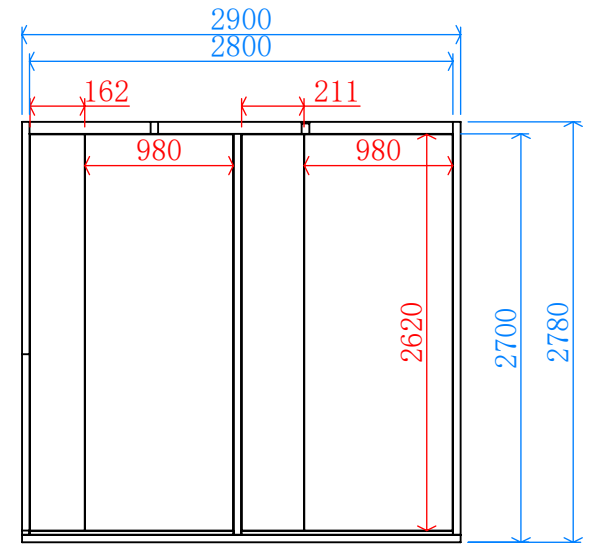


B

DESIGN	FYJ	 Airkey Envirotech Co.,Ltd
DATE	2026/1/8	
REVIEW		
RATIO	1:50	Item : FSP-N-A19 (9. 2+9. 2) -F
DWG No.	5	

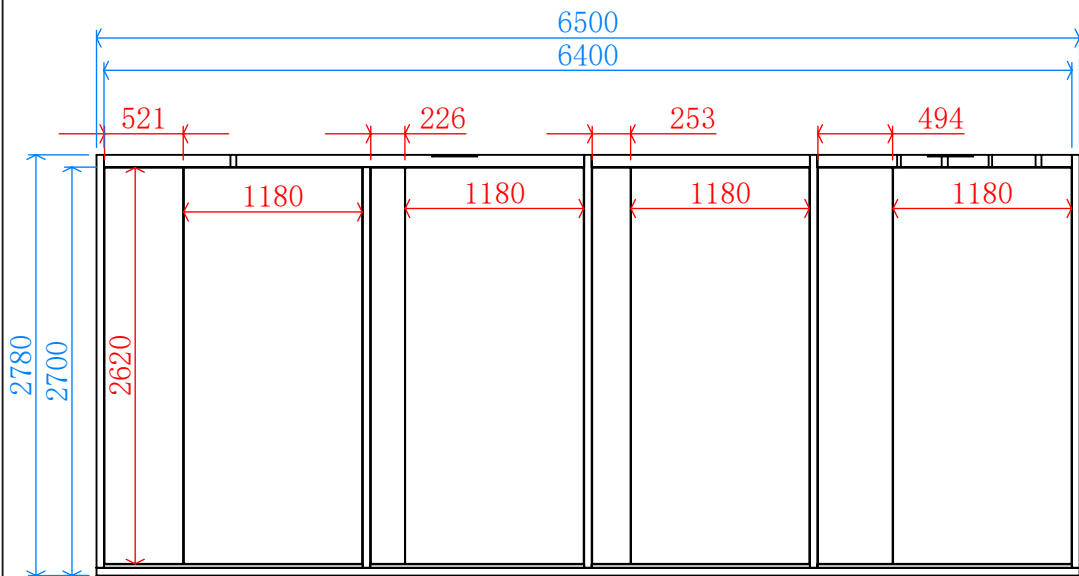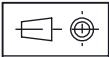


C

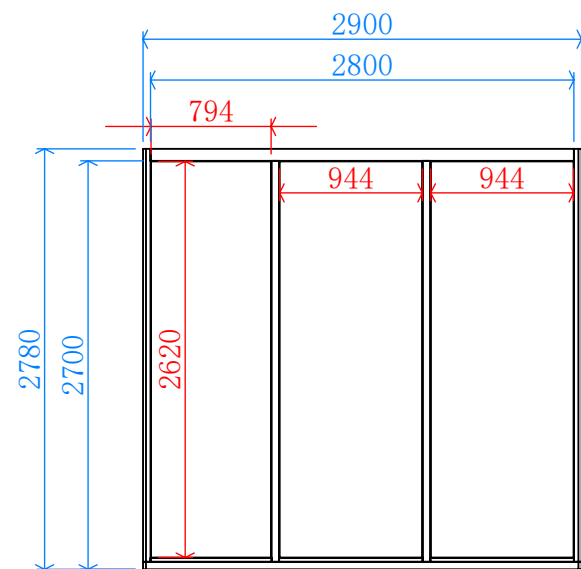


D


DESIGN	FYJ	 Airkey Envirotech Co.,Ltd
DATE	2026/1/8	
REVIEW		
RATIO	1:50	Item : FSP-N-A19 (9. 2+9. 2) -F
DWG No.	6	

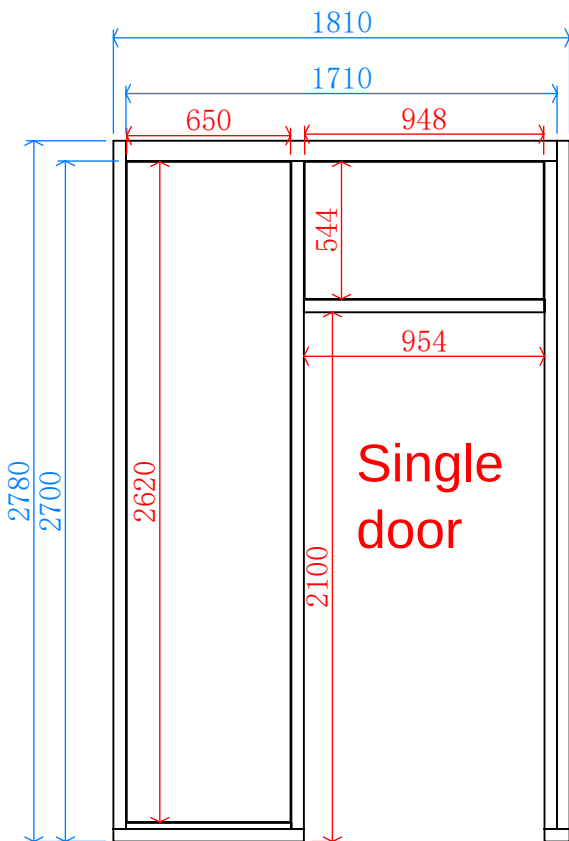

E

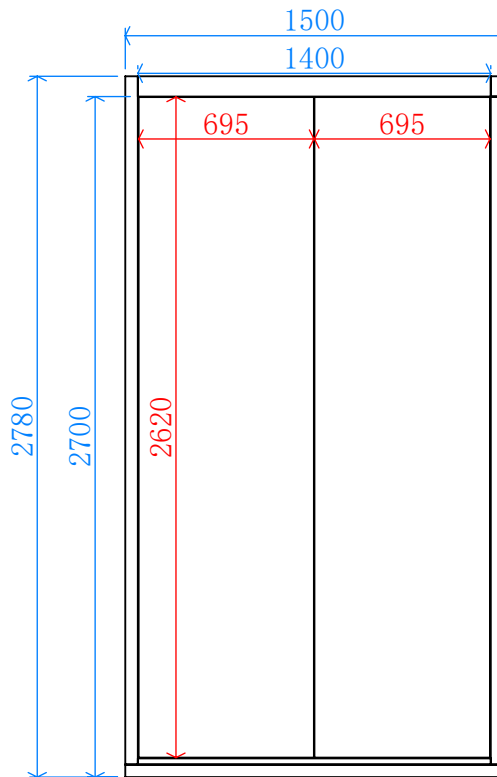


F

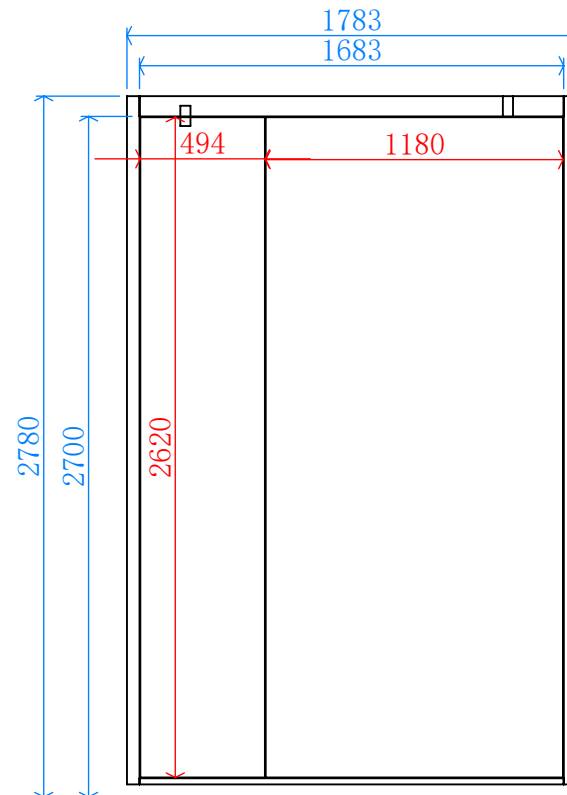


I/J

DESIGN	FYJ	 Airkey Envirotech Co.,Ltd
DATE	2026/1/8	
REVIEW		
RATIO	1:30	Item : FSP-N-A19 (9. 2+9. 2) -F
DWG No.	7	

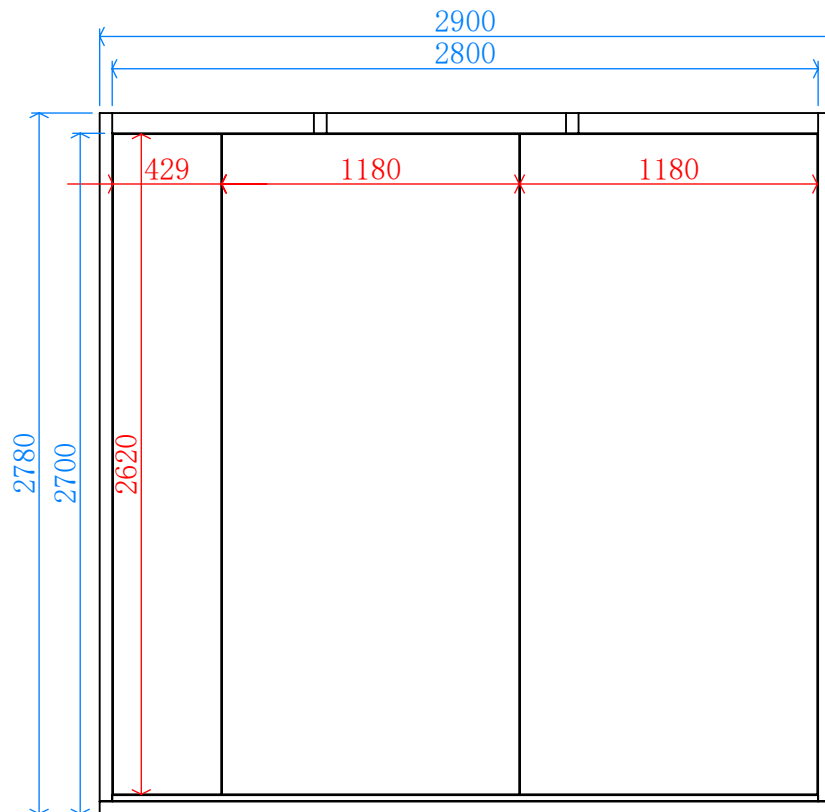


G

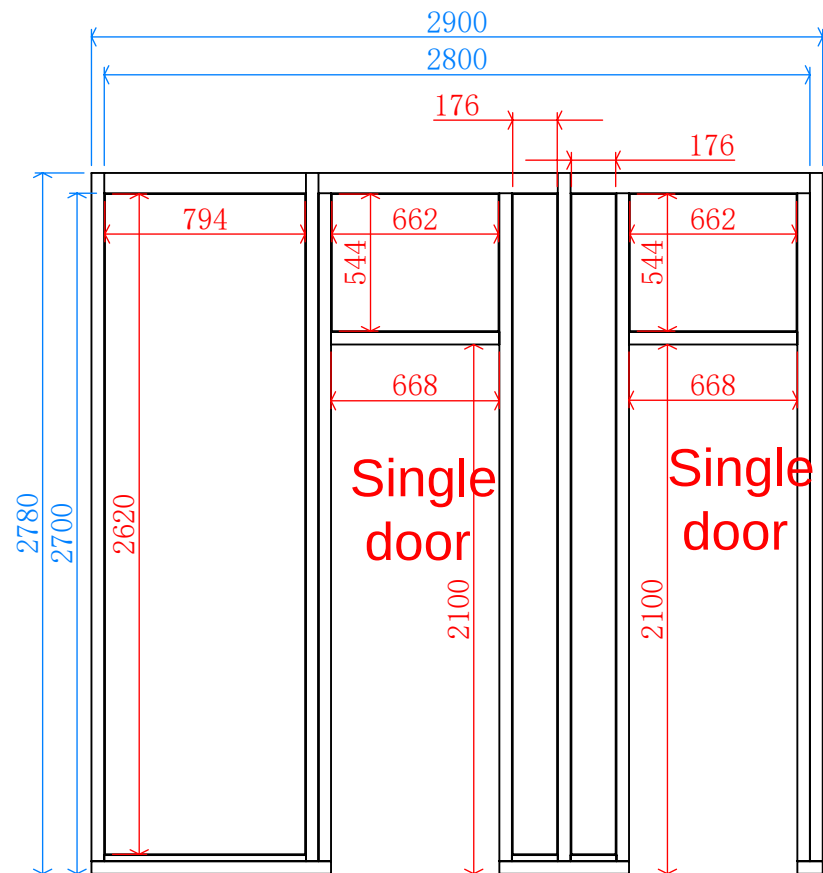

H

DESIGN	FYJ	 Airkey Envirotech Co.,Ltd
DATE	2026/1/8	
REVIEW		
RATIO	1:30	Item : FSP-N-A19 (9. 2+9. 2) -F
DWG No.	8	

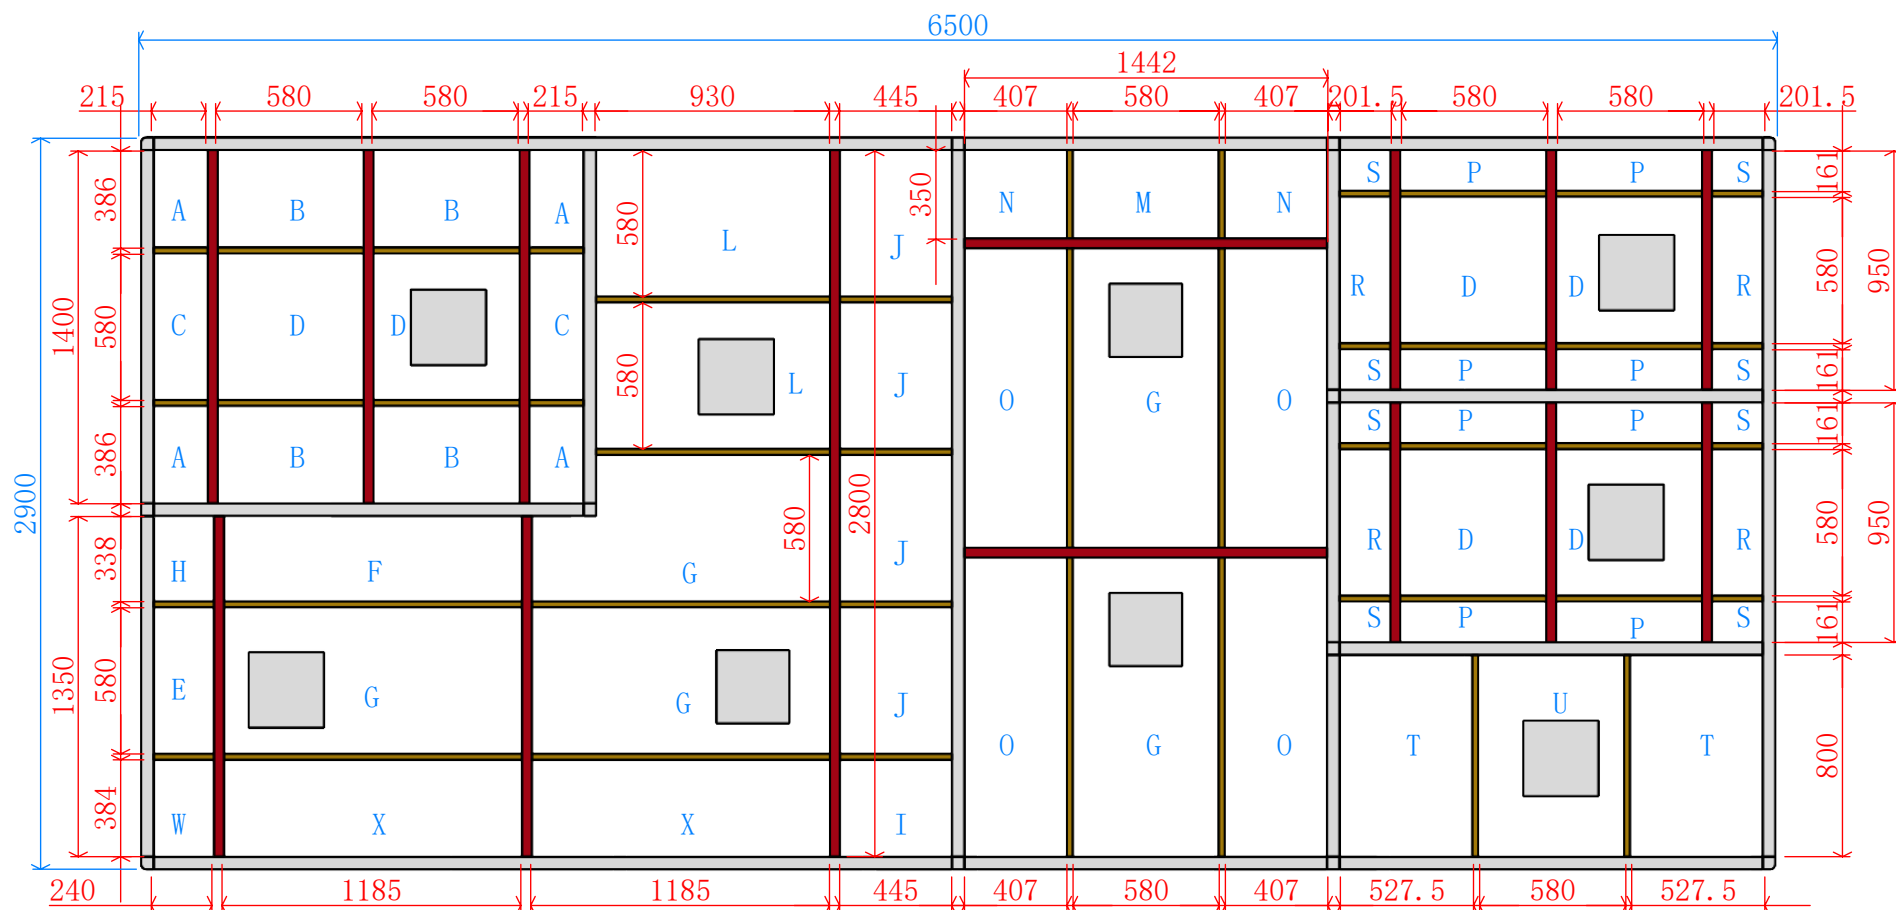

Ceiling Panels:

200*375mm=4pcs (A) 570*375mm=4pcs (B) 200*570mm=2pcs (C)
570*570mm=2pcs (D) 230*570mm=1pcs (E) 1170*330mm=1pcs (F)
1170*570mm=5pcs (G) 230*330mm=1pcs (H) 435*375mm= 1pcs (I)
435*570mm=4pcs (J) 920*570mm= 2pcs (L) 395*340mm=2pcs (N)
570*340mm=1pcs (M) 395*1170mm=4pcs (O) 570*150mm=8pcs (P)
190*570mm=4pcs (R) 190*150mm=8pcs (S) 515*790mm=2pcs (T)
570*790mm=1pcs (U) 230*375mm=1pcs (W) 1170*375mm=2pcs (X)



Sub-ceiling Grids:

24*40*240mm=4pcs 24*40*580mm=12pcs 24*40*190mm=2pcs
24*40*930mm=2pcs 24*40*445mm=4pcs 24*40*1185mm=8pcs
24*40*350mm=2pcs 24*40*201.5mm=8pcs 24*40*800mm=2pcs

Main Ceiling Grids:


40*80*1400mm=3pcs 40*80*1350mm=2pcs 40*80*2800mm=1pcs
40*80*1442mm=2pcs 40*80*950mm =6pcs

DESIGN	FYJ	 Airkey Envirotech Co.,Ltd
DATE	2026/1/8	
REVIEW		Item : FSP-N-A19 (9. 2+9. 2) -F
RATIO	1:30	
DWG No.	9	

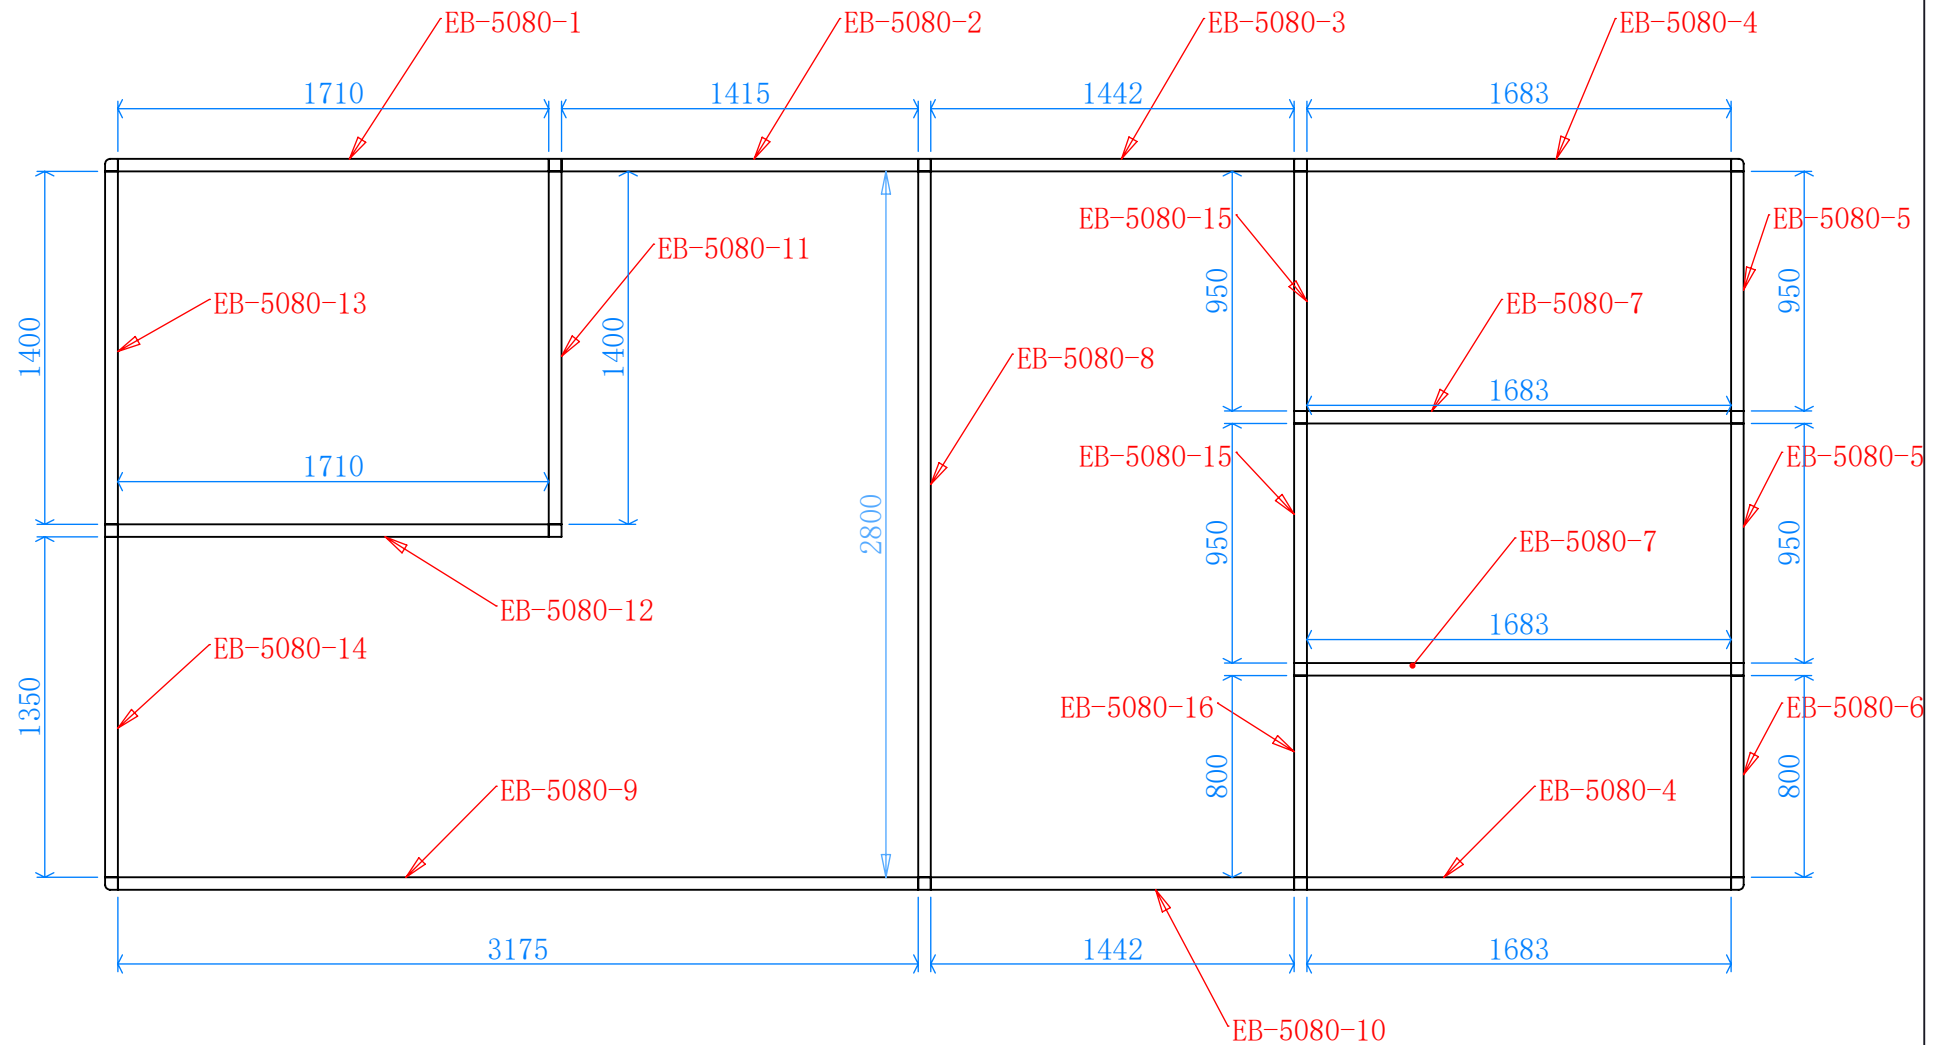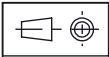


EDGE BEAM ASSEMBLY

DESIGN	FYJ	 Airkey Envirotech Co.,Ltd
DATE	2026/1/8	
REVIEW		
RATIO	1:30	Item : FSP-N-A19 (9. 2+9. 2) -F
DWG No.	11	

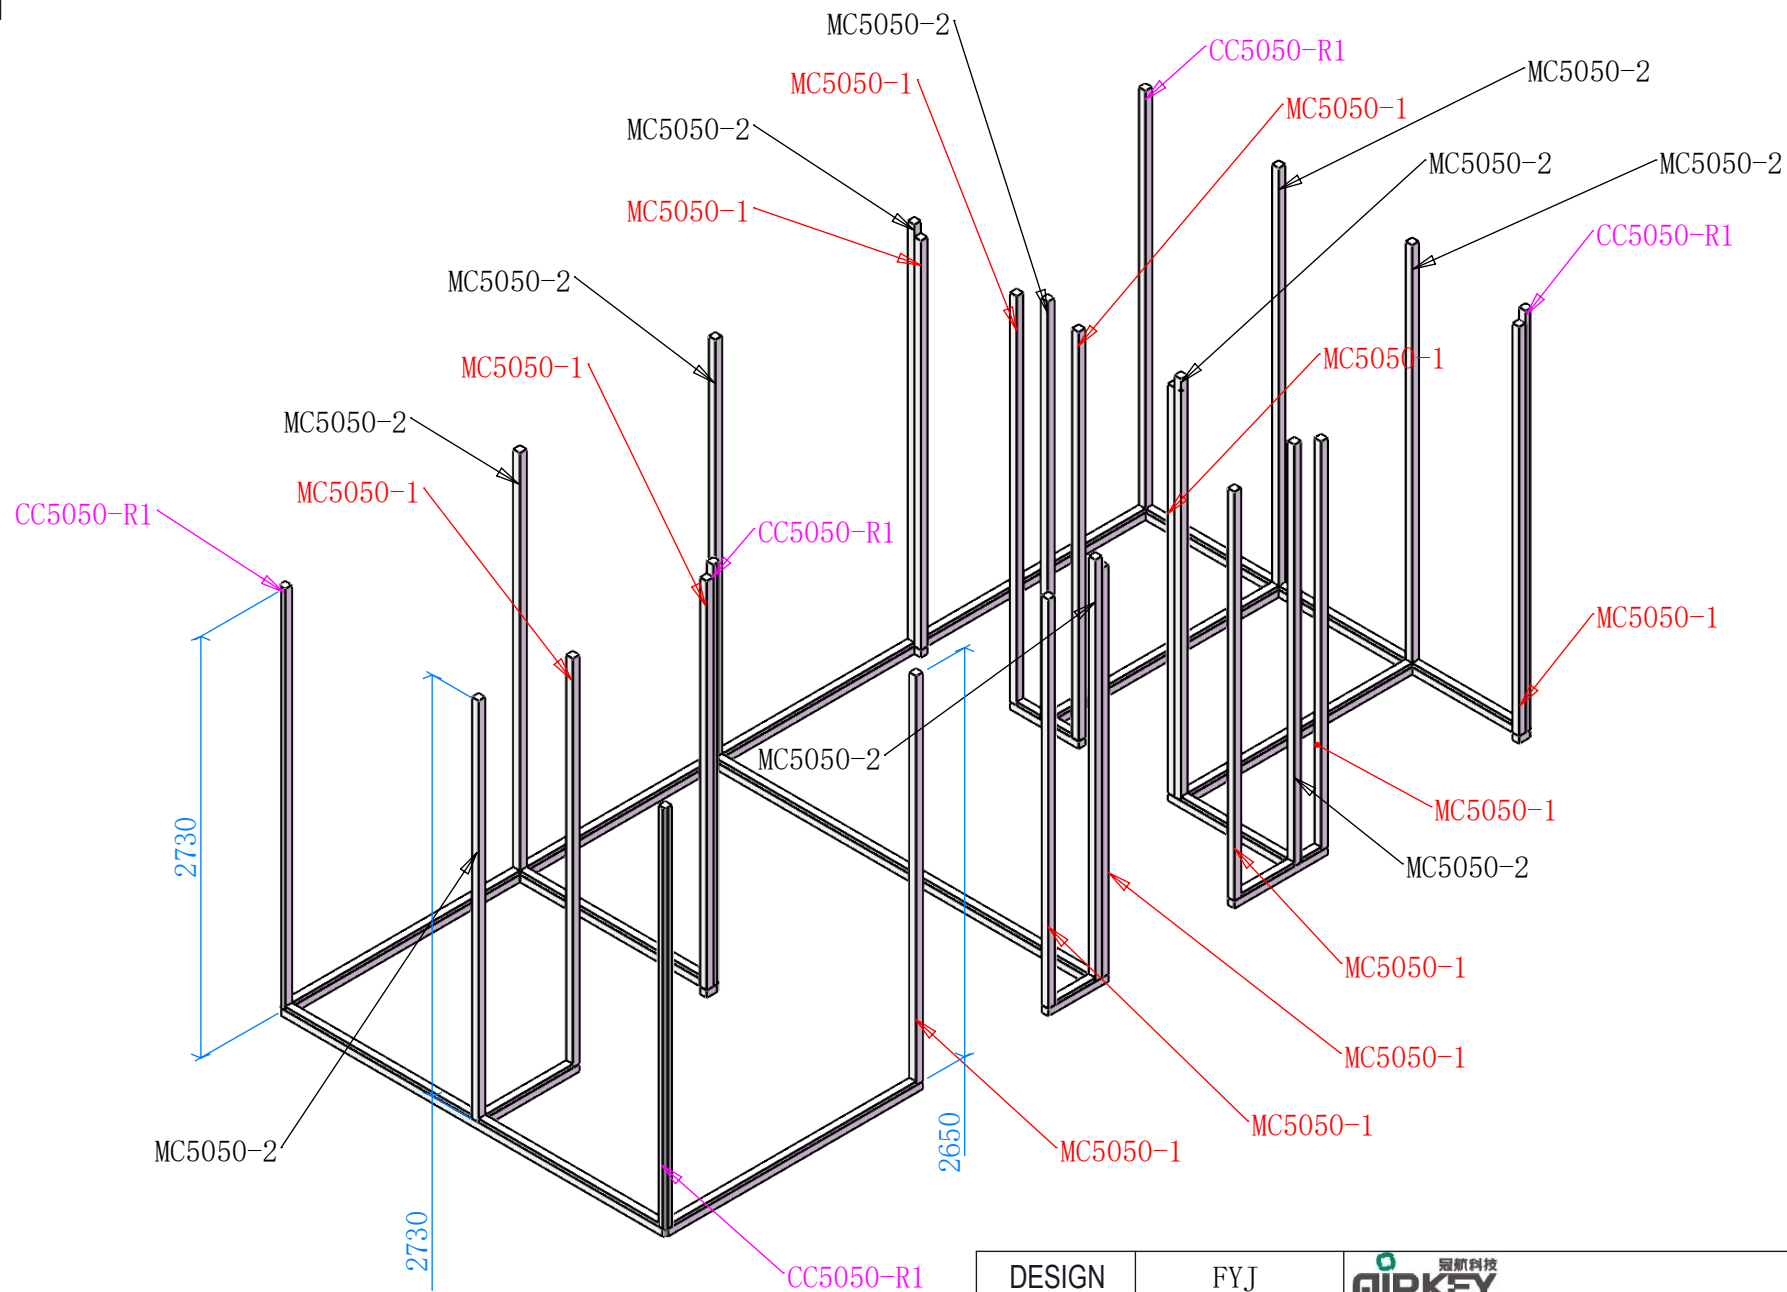


COLUMN ASSEMBLY

DESIGN	FYJ	 Airkey Envirotech Co.,Ltd
DATE	2026/1/8	
REVIEW		Item : FSP-N-A19 (9. 2+9. 2) -F
RATIO	1:40	
DWG No.	12	

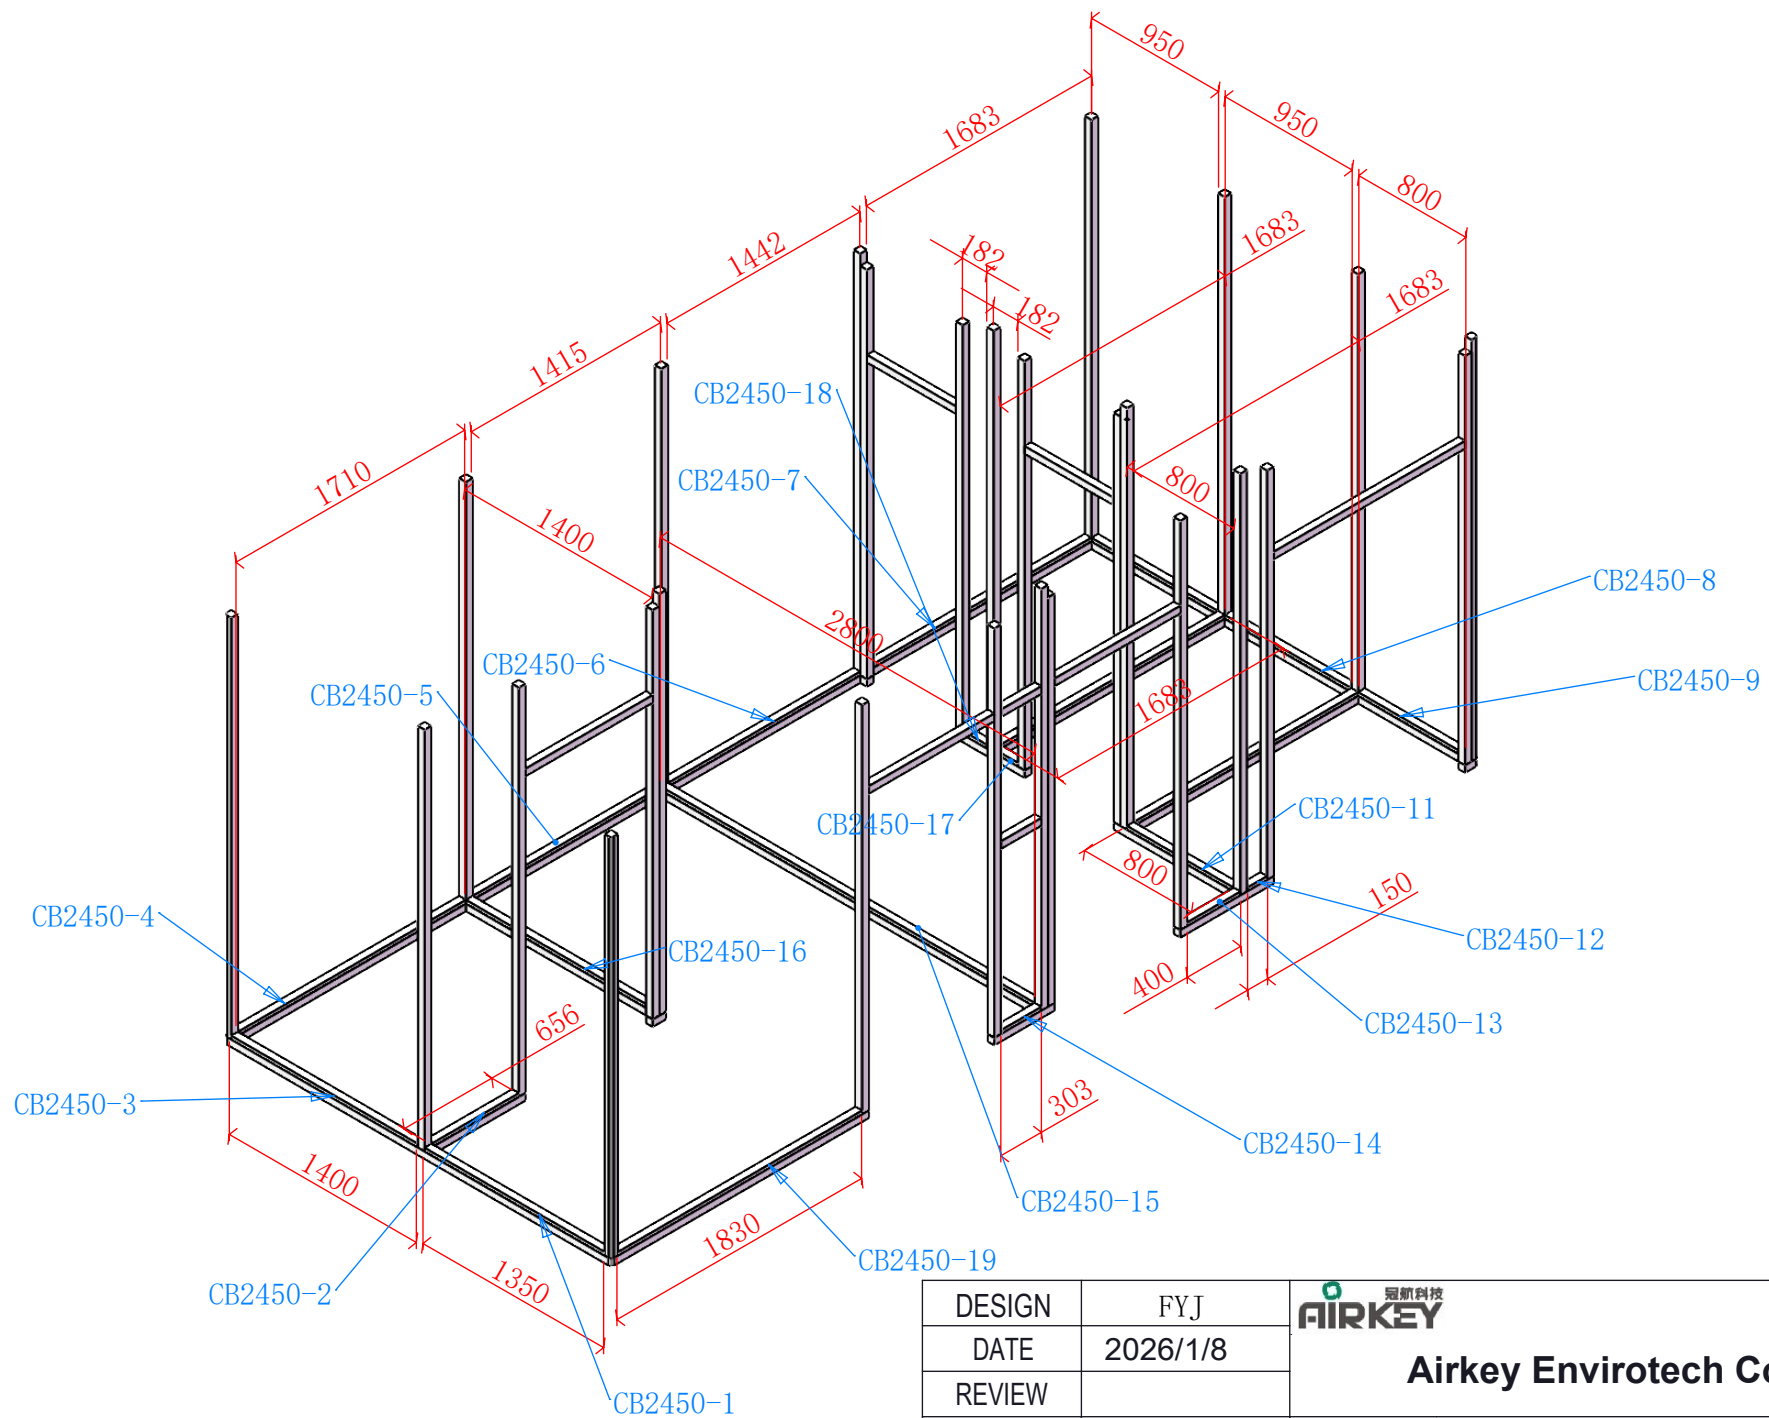

BRACING FRAME ASSEMBLY

DESIGN	FYJ	 Airkey Envirotech Co.,Ltd
DATE	2026/1/8	
REVIEW		
RATIO	1:40	Item : FSP-N-A19 (9. 2+9. 2) -F
DWG No.	13	

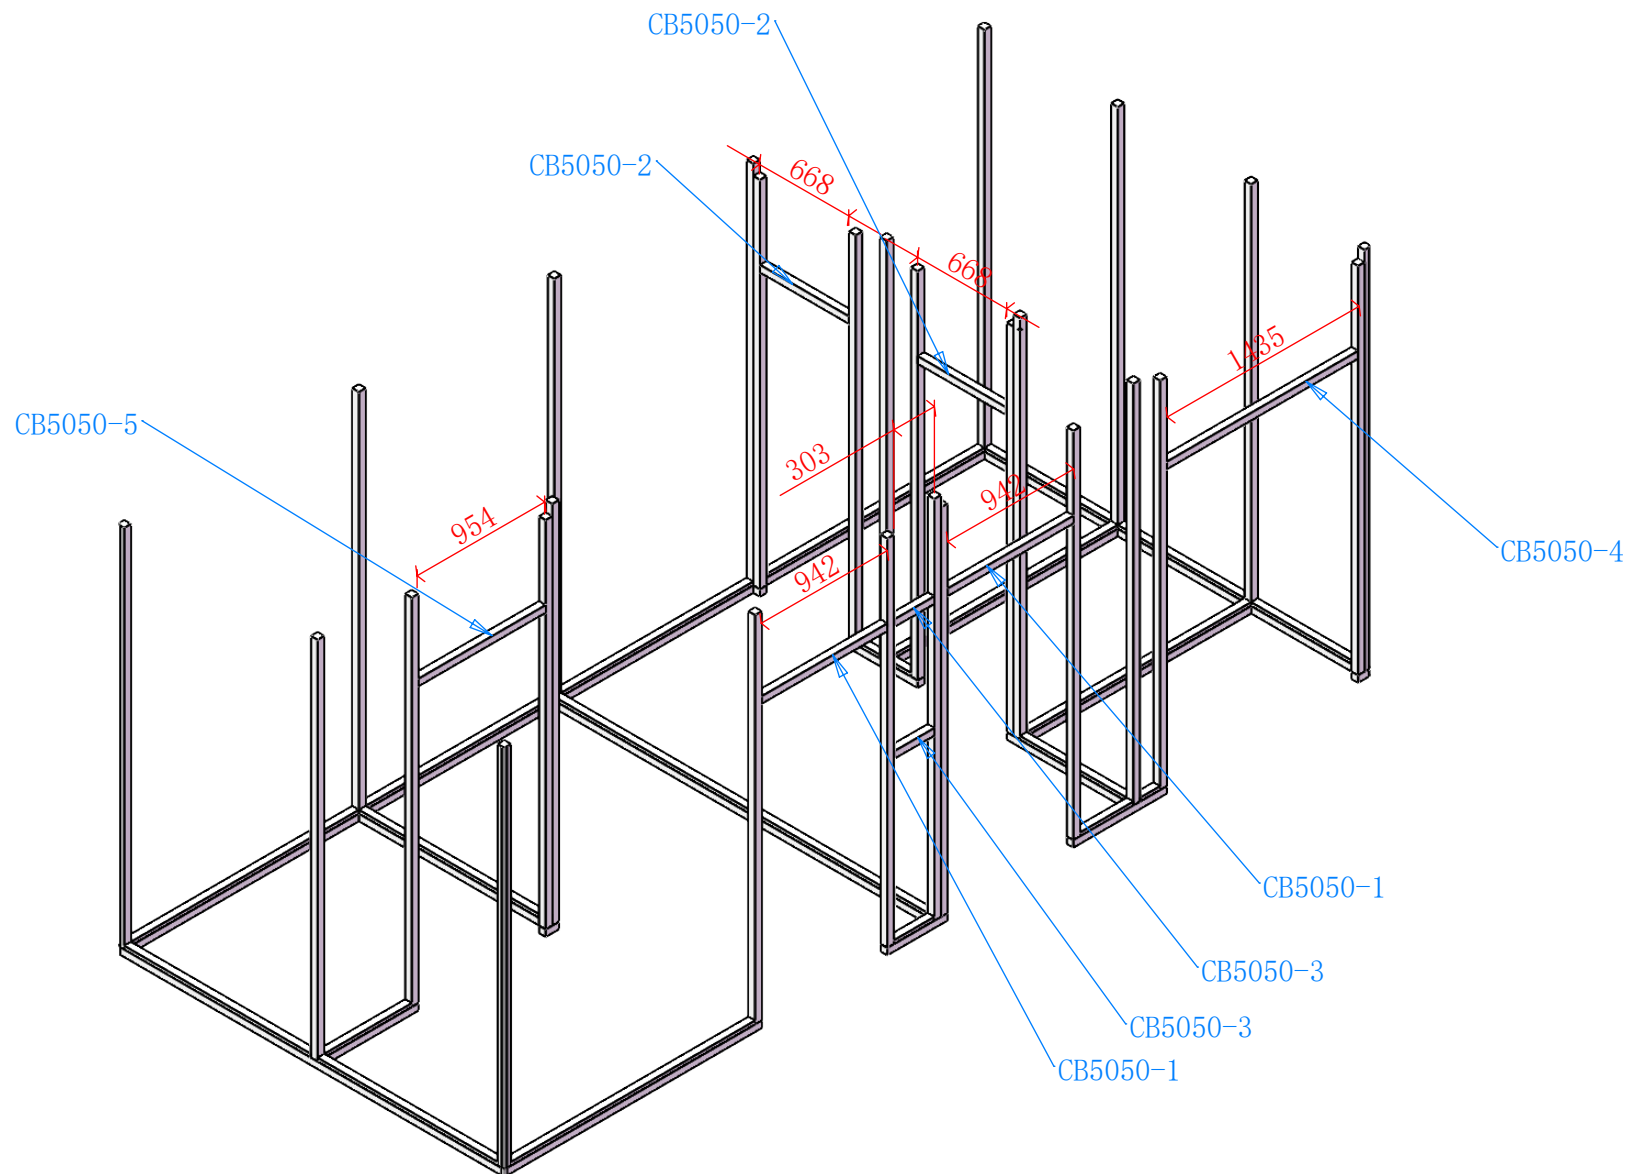

BRACING FRAME ASSEMBLY

DESIGN	FYJ	 Airkey Envirotech Co.,Ltd
DATE	2026/1/8	
REVIEW		Item : FSP-N-A19 (9. 2+9. 2) -F
RATIO	1:40	
DWG No.	14	