


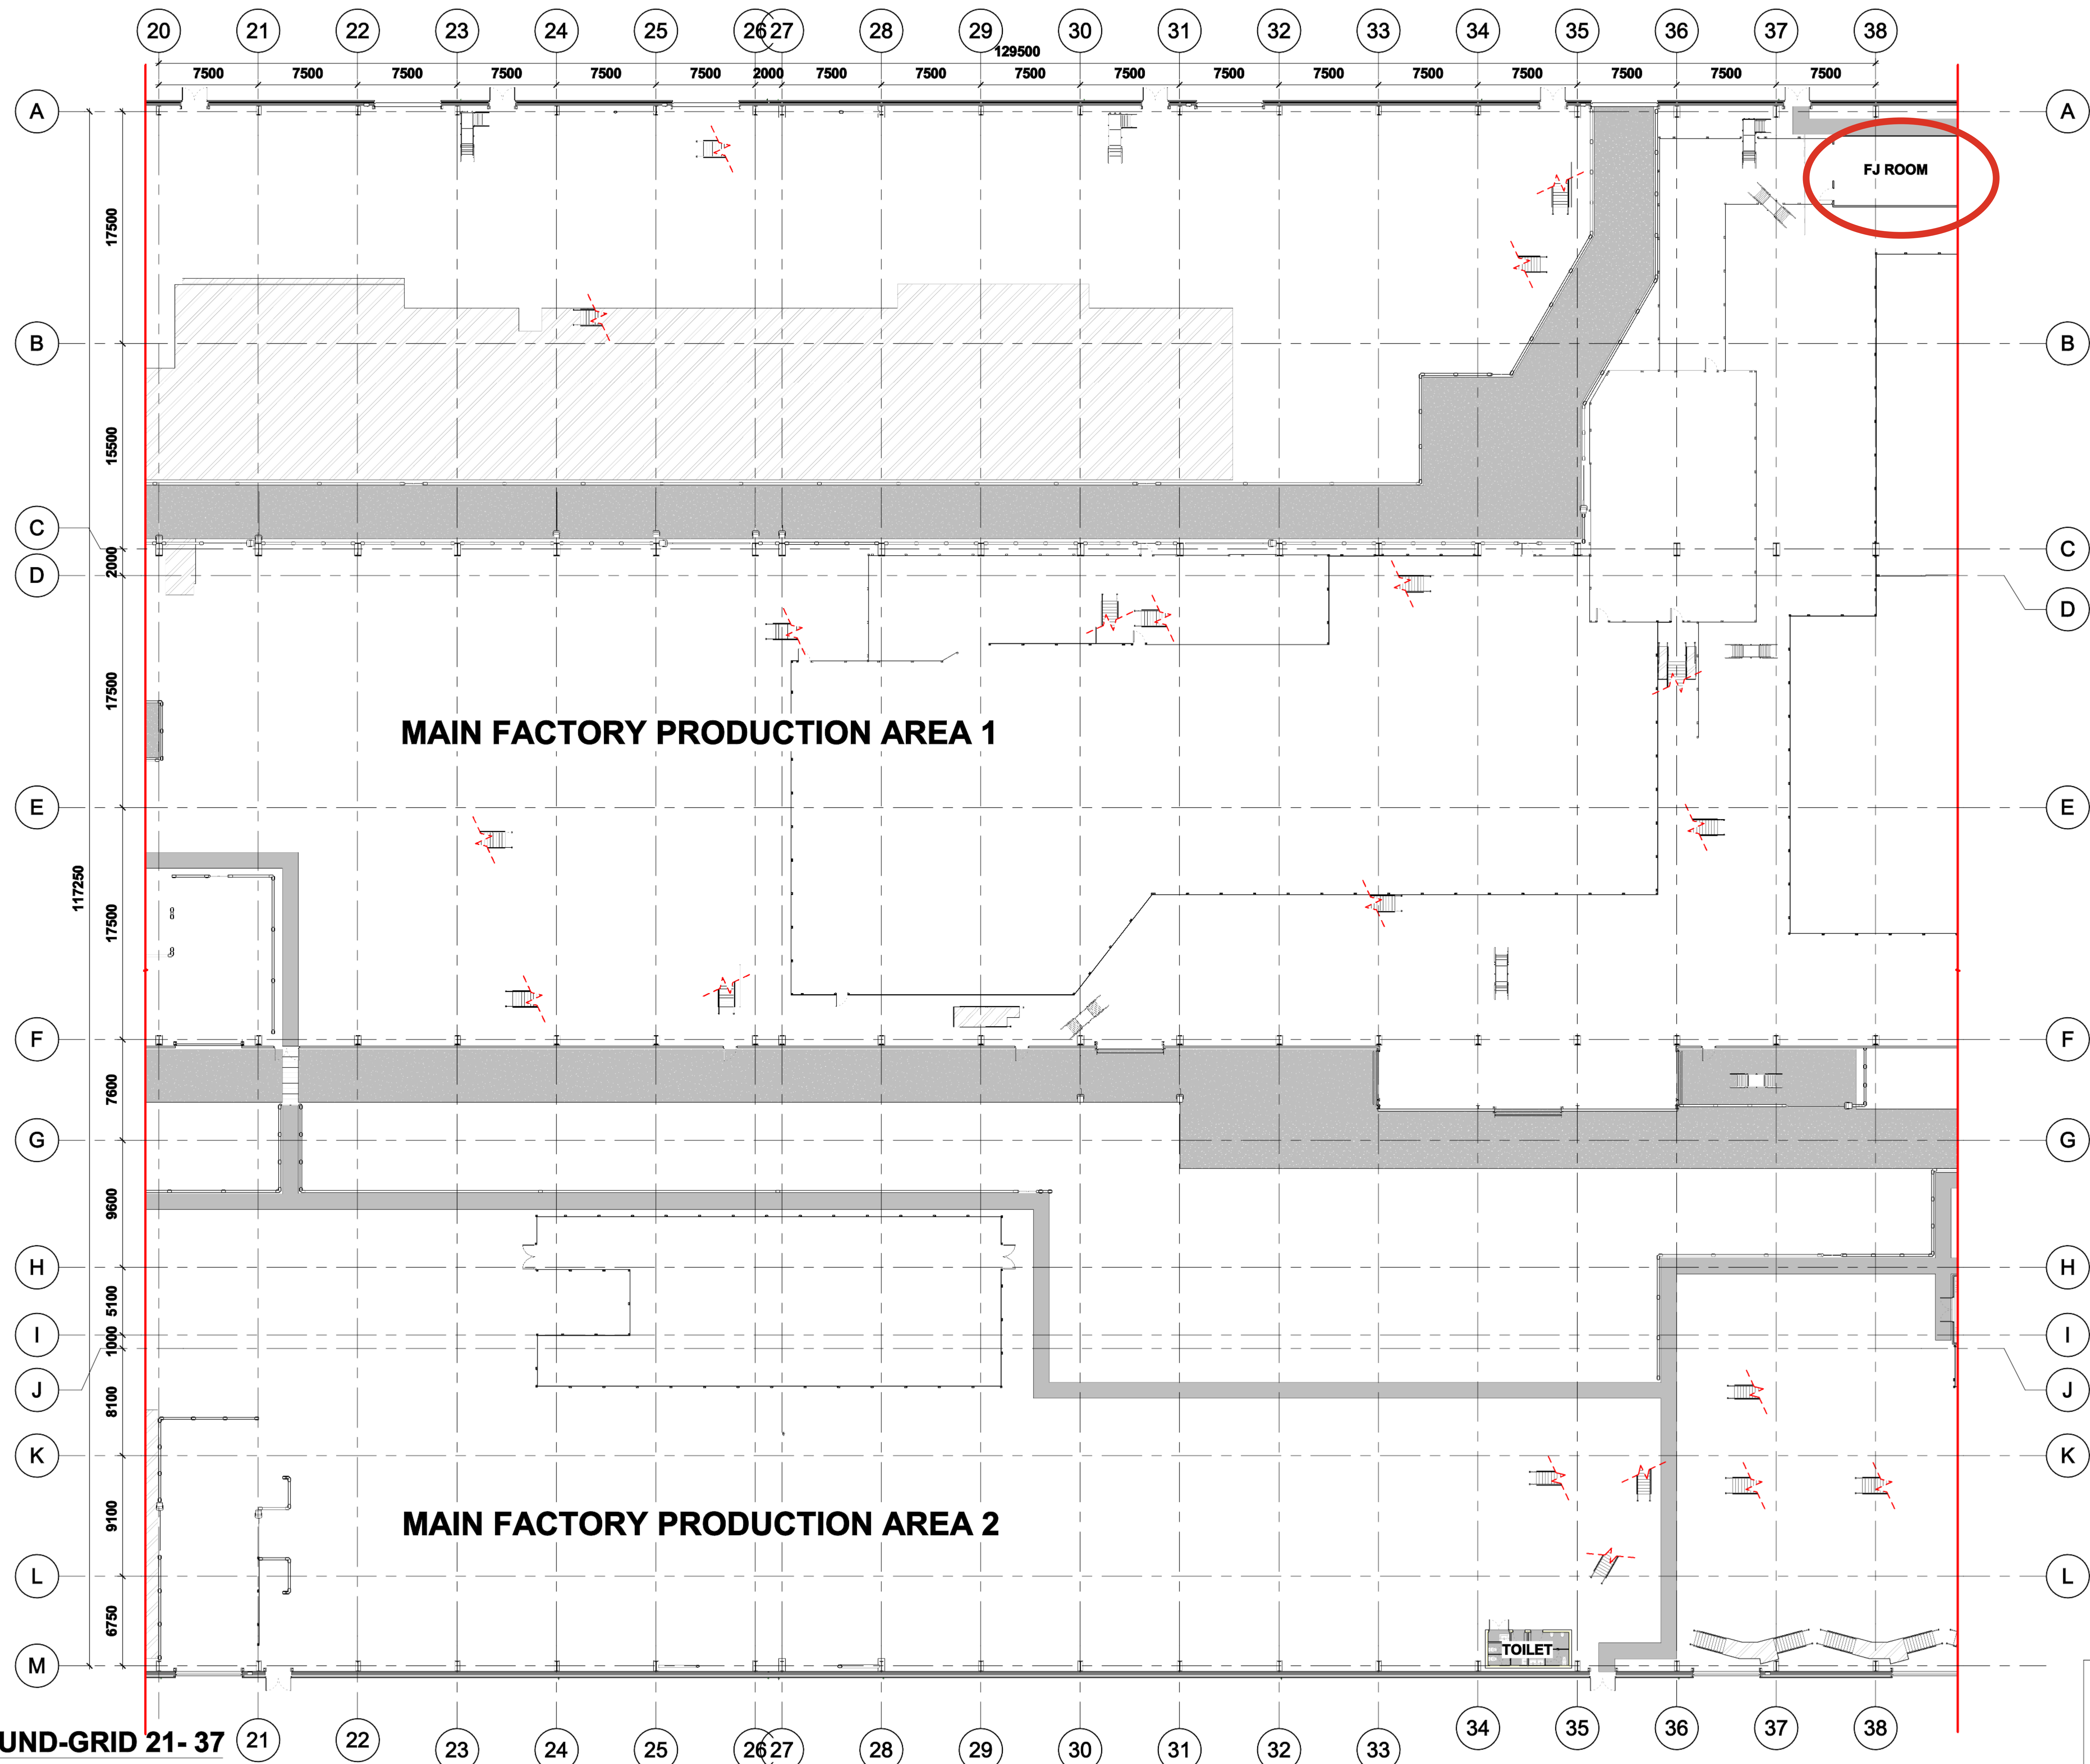

1 **GA -**
1 : 250

A1



Copyright EDA Architects Ltd. The Construction (Design and Management) Regulations 2015 apply to this project. Please refer to the 'Pre-Construction Information', 'Construction Phase Plan' and other relevant documents. All dimensions in millimeters. This drawing is subject to statutory approval (planning, building control etc).



eda
ARCHITECTS

EDA Architects Ltd
Omagh Enterprise Centre,
41 Gortrush Ind Est,
Omagh BT78 5LU
eoghan@eda-architects.com

[illegible]

DATE	DESCRIPTION	CHK	DRN
STATUS			
54			
PROJECT			
DEEP SEA CABLE FACTORY			
PROJECT ADDRESS			
PORT OF NIGG, TAIN			
DISCIPLINE			
ARCHITECTURAL			
DOWG TITLE			
PLAN GRID 21 - 37			

DWG NO.	
264- EDA- MF- 00- DR- AR- 11302	
STATUS CODE	
34	
PROJECT NO.	DATE
264	04.02.25
DRAWN / CHECKED	SCALE NO.
LF/ ED	1 : 250

