
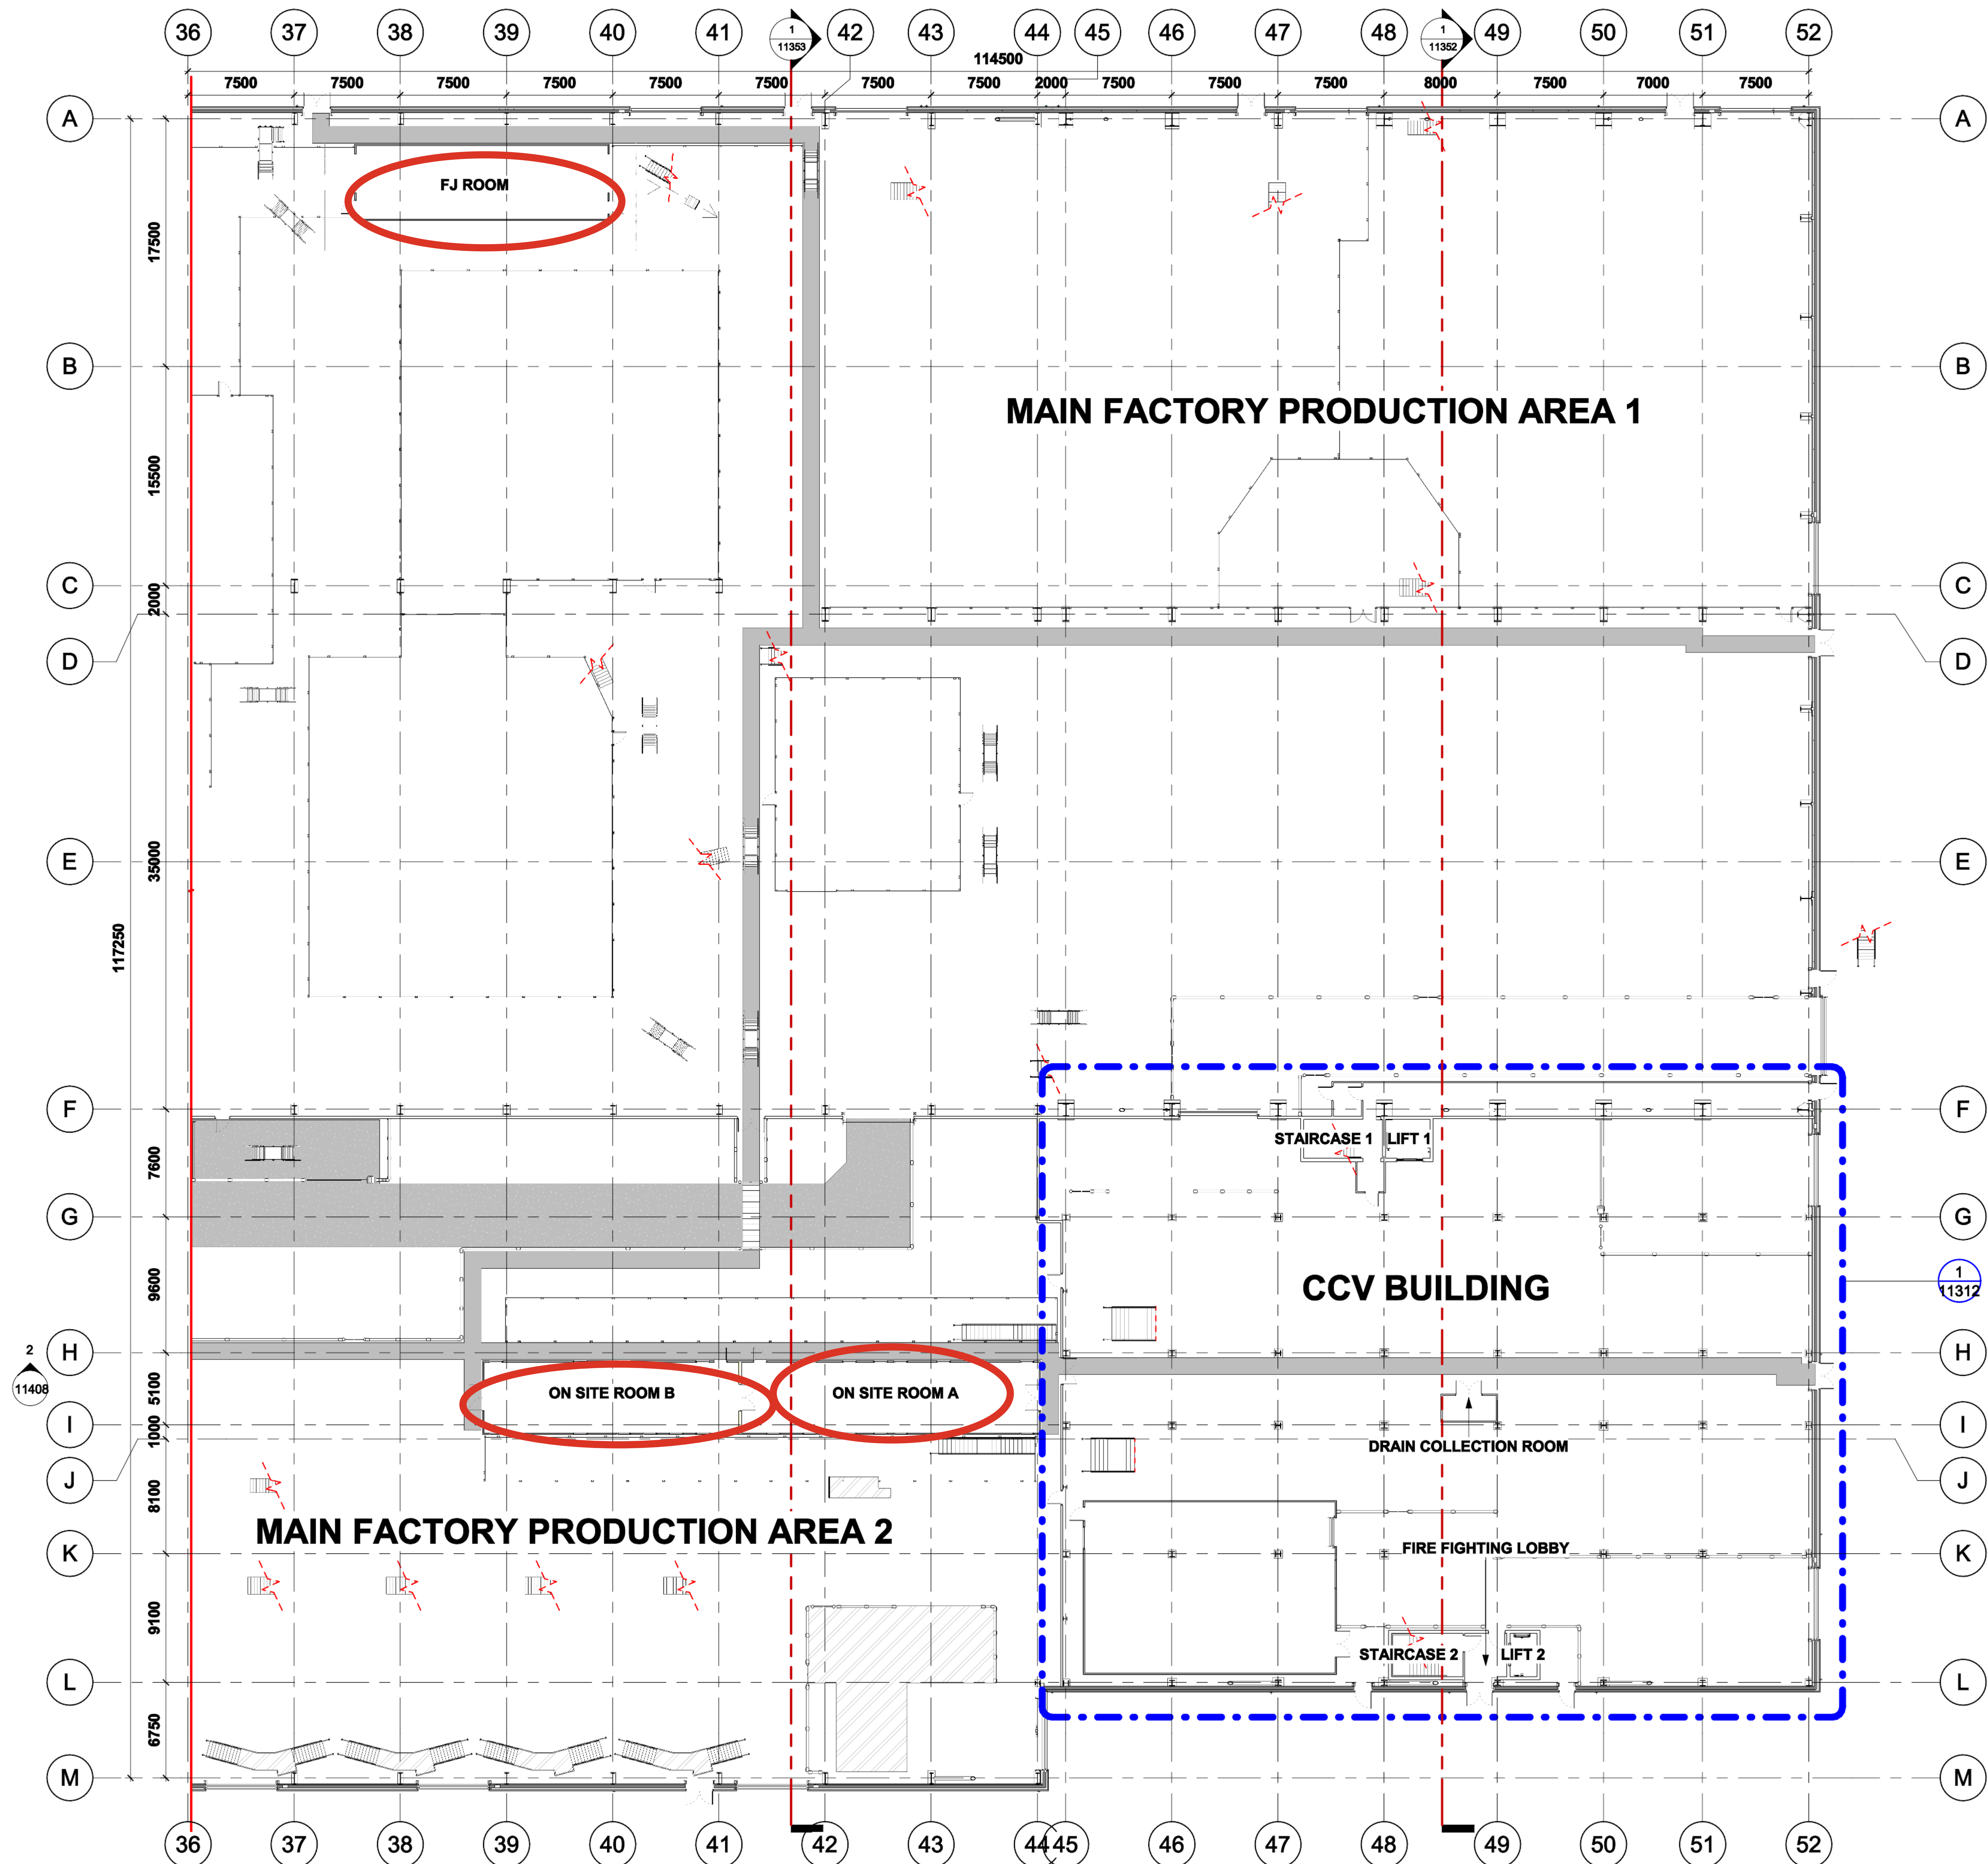


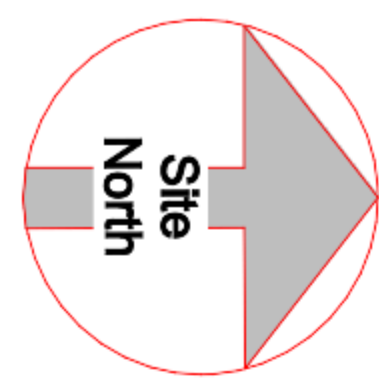


1 GA - GROUND-GRID 37- 52
1 : 250

ALL DIMENSIONS TO BE CHECKED ON SITE.
NO DIMENSIONS TO BE SCALED FROM THIS
DRAWING. DRAWING IS TO BE USED IN
CONJUNCTION WITH RELEVANT
CONSULTANT DRAWINGS

A1


SITE KEY PLAN

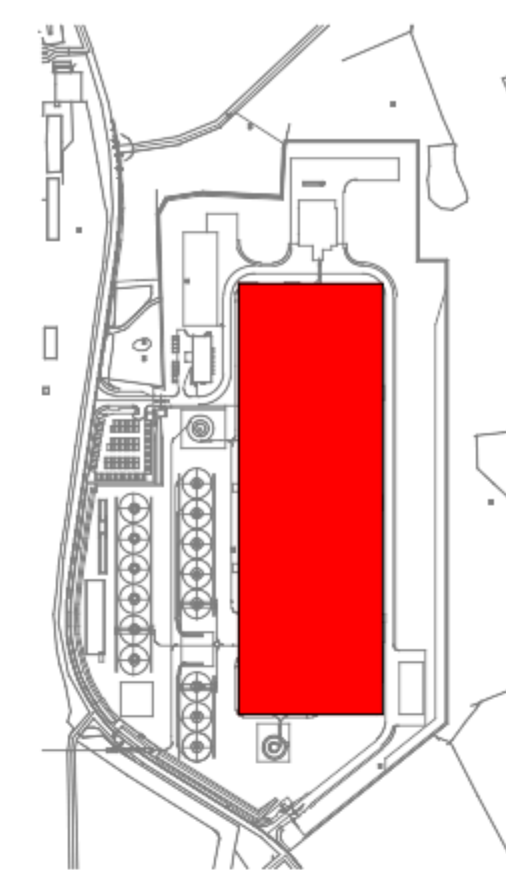

LEGEND

© Copyright EDA Architects Ltd. The Construction (Design and Management) Regulations 2015 apply to this project. Please refer to the 'Pre-Construction Information', 'Construction Phase Plan' and other relevant documents. All dimensions in millimeters. This drawing is subject to statutory approval (planning, building control etc)

KEY PLAN

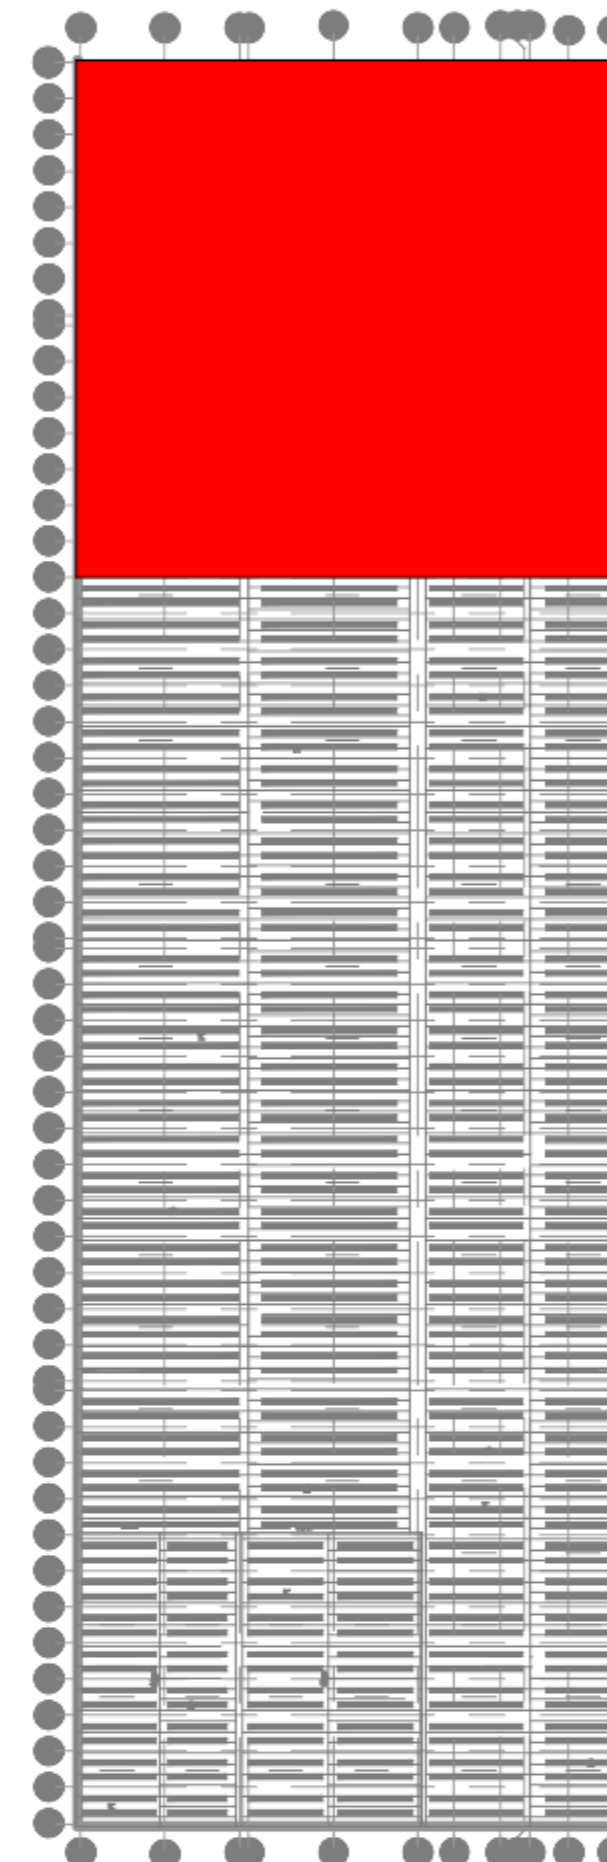

**SUMITOMO
ELECTRIC**

SEI, Kuji-cho
Hitachi City Japan

eda

EDA Architects Ltd
Omagh Enterprise Centre,
41 Gortrash Ind Est,
Omagh BT78 8LU
eoghan@eda-architects.com

REVISIONS

REV	DATE	DESCRIPTION	CHK	DN
1	11312			

STATUS

S4

PROJECT

DEEP SEA CABLE FACTORY

PROJECT ADDRESS

PORT OF NIGG, TAIN

DISCIPLINE

ARCHITECTURAL

DWG TITLE

PLAN GRID 37 - 52

DWG NO.

S264- EDA- MF- 00- DR- AR- 11303

STATUS CODE

S4

PROJECT NO.

S264

DRAWN / CHECKED

LF/ ED

DATE

04.02.25

SCALE NO.

1 : 250

REVISION NUMBER

**EUROPLAN
GROUP**

Parkview House, Beechill Office Campus,
Clonskeagh, Dublin 4, Eire.
Tel: +353 1 2606578
staprojectteam@europlanservices.com